


E-104:
Calentador de la fase orgánica
Coraza: Vapor de caldera
Tubos: Fase orgánica

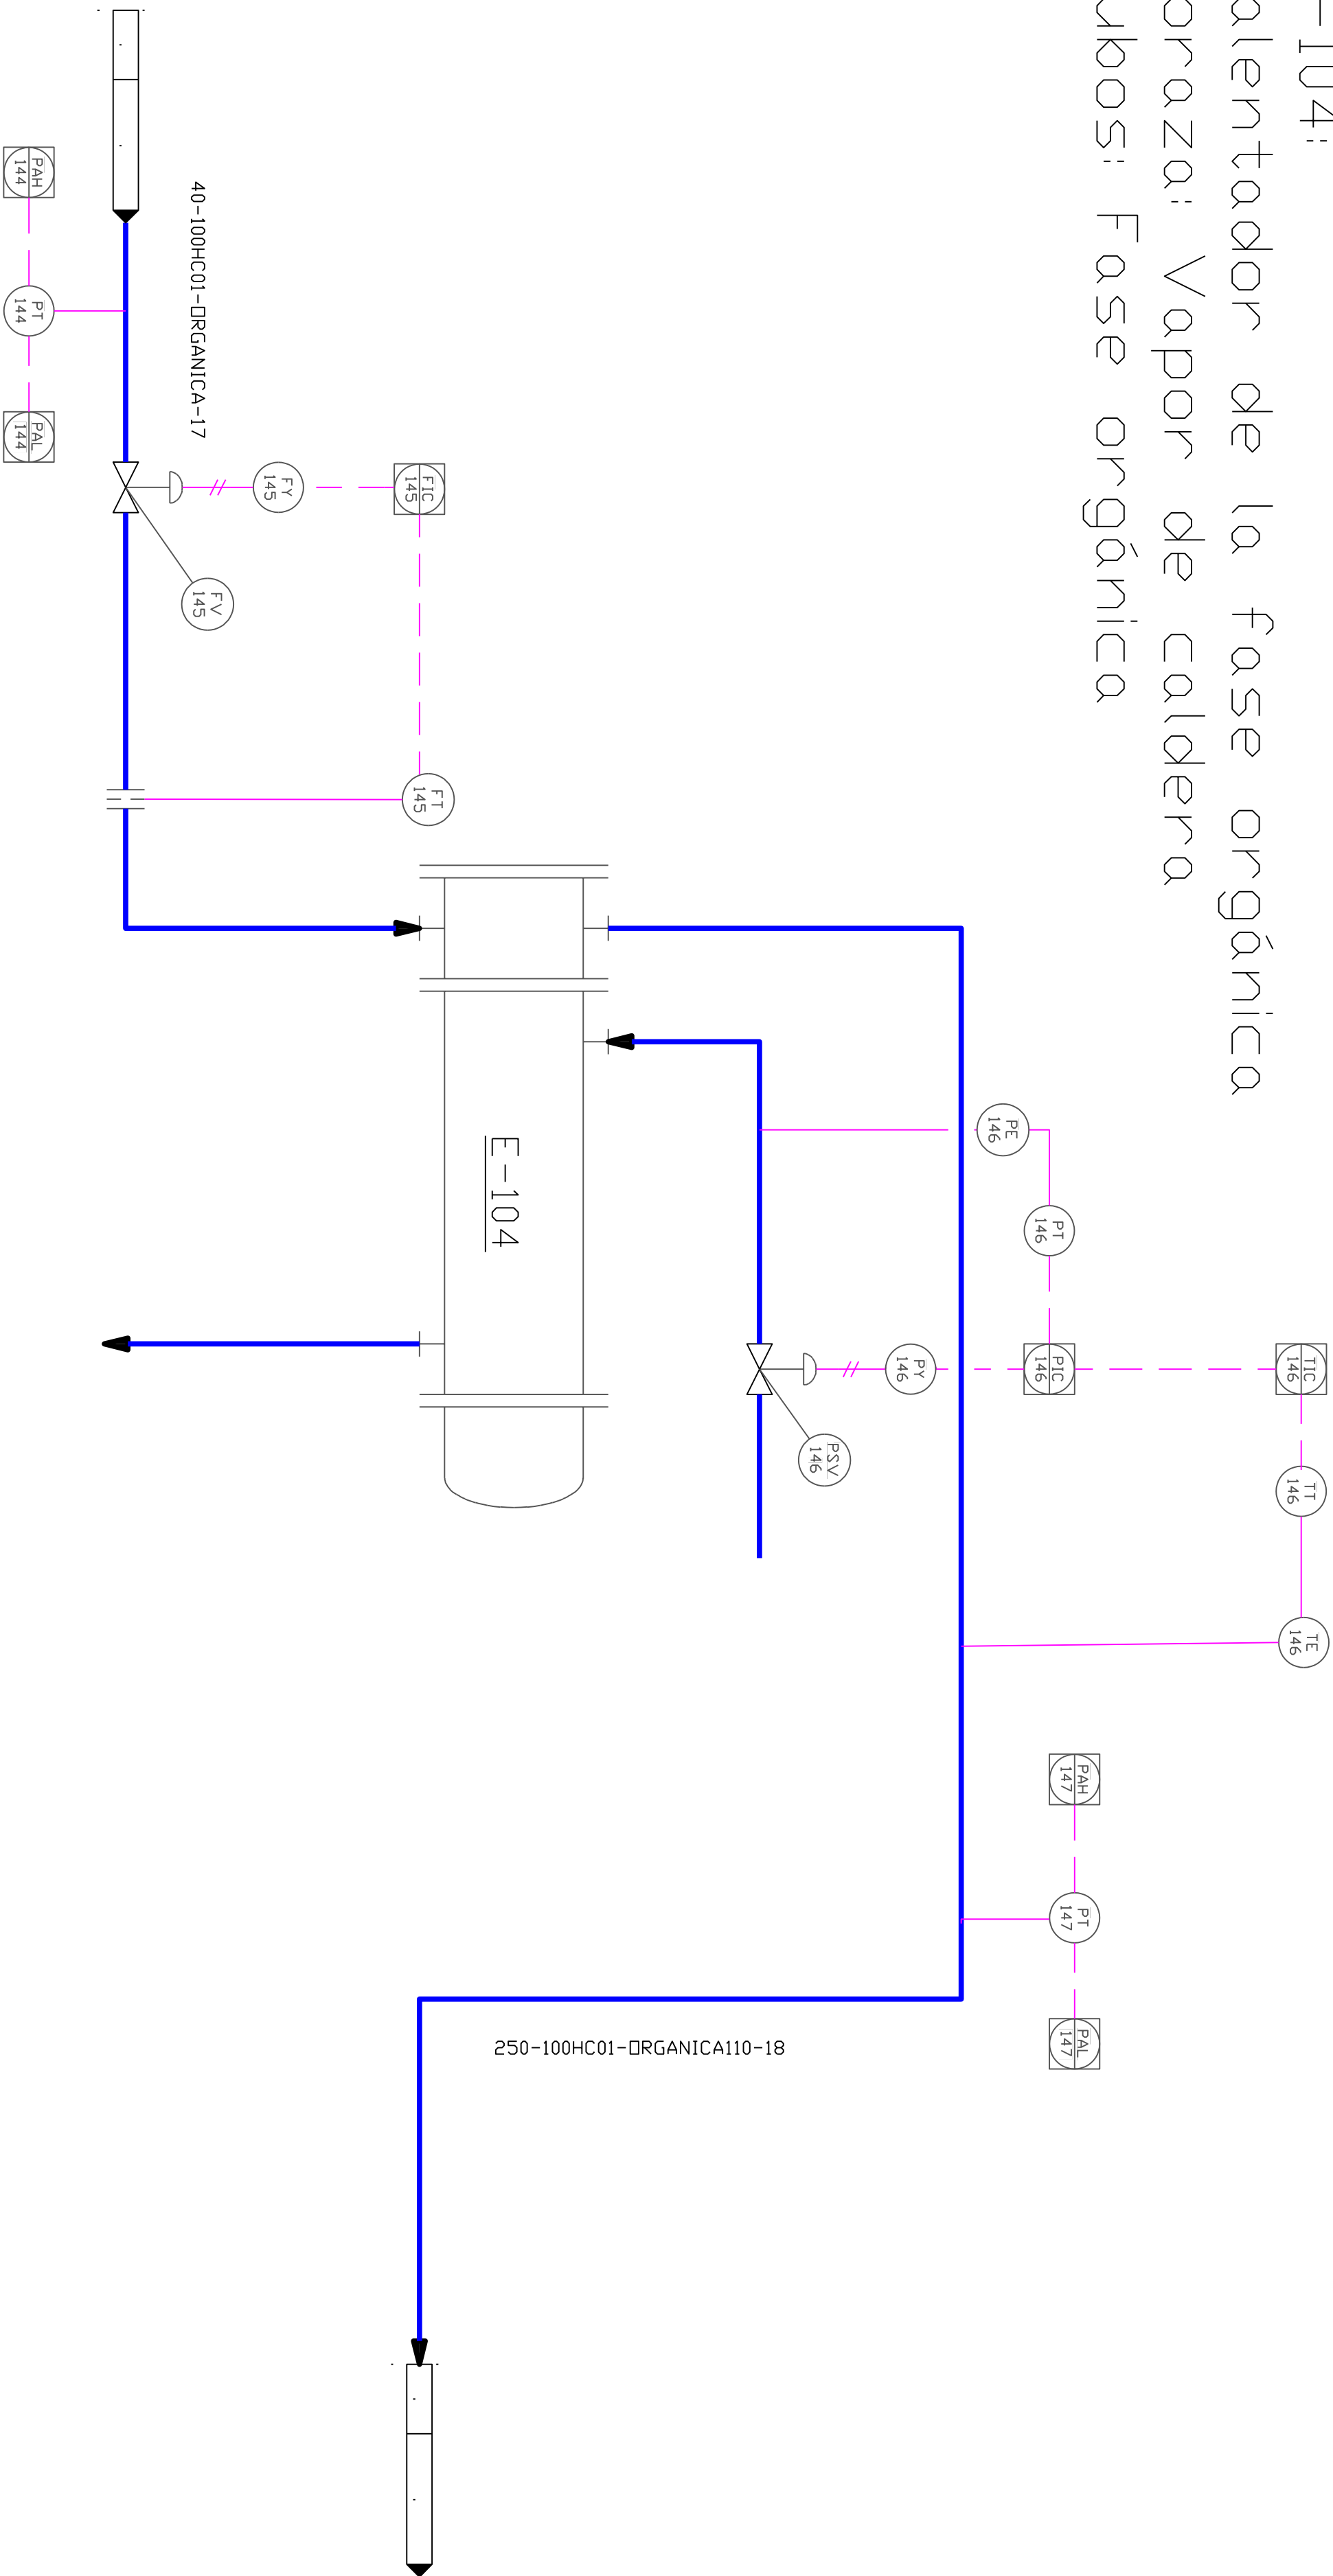

General Notes

- Valvula de control
- Intercambiador de calor
- TE Elemento de temperatura
- PAH Alarma de presión baja
- FIC Controlador indicador de flujo
- FY Convertidor de señal de flujo
- FT Transmisor de flujo
- PT Transmisor de presión
- PAH Alarma de presión alta
- PE Elemento de presión
- PIC Controlador indicador de presión
- FY Convertidor de señal de presión
- TIC Controlador indicador de temperatura
- TT Transmisor de temperatura

No.	Revision/Issue	Date

Calentador fase
orgánica

Project Name and Address

ANILINA
Planta de Anilina

Area ###

Drawing Number

###

Author

ESQIE IPN