


Columna de destilación T-101

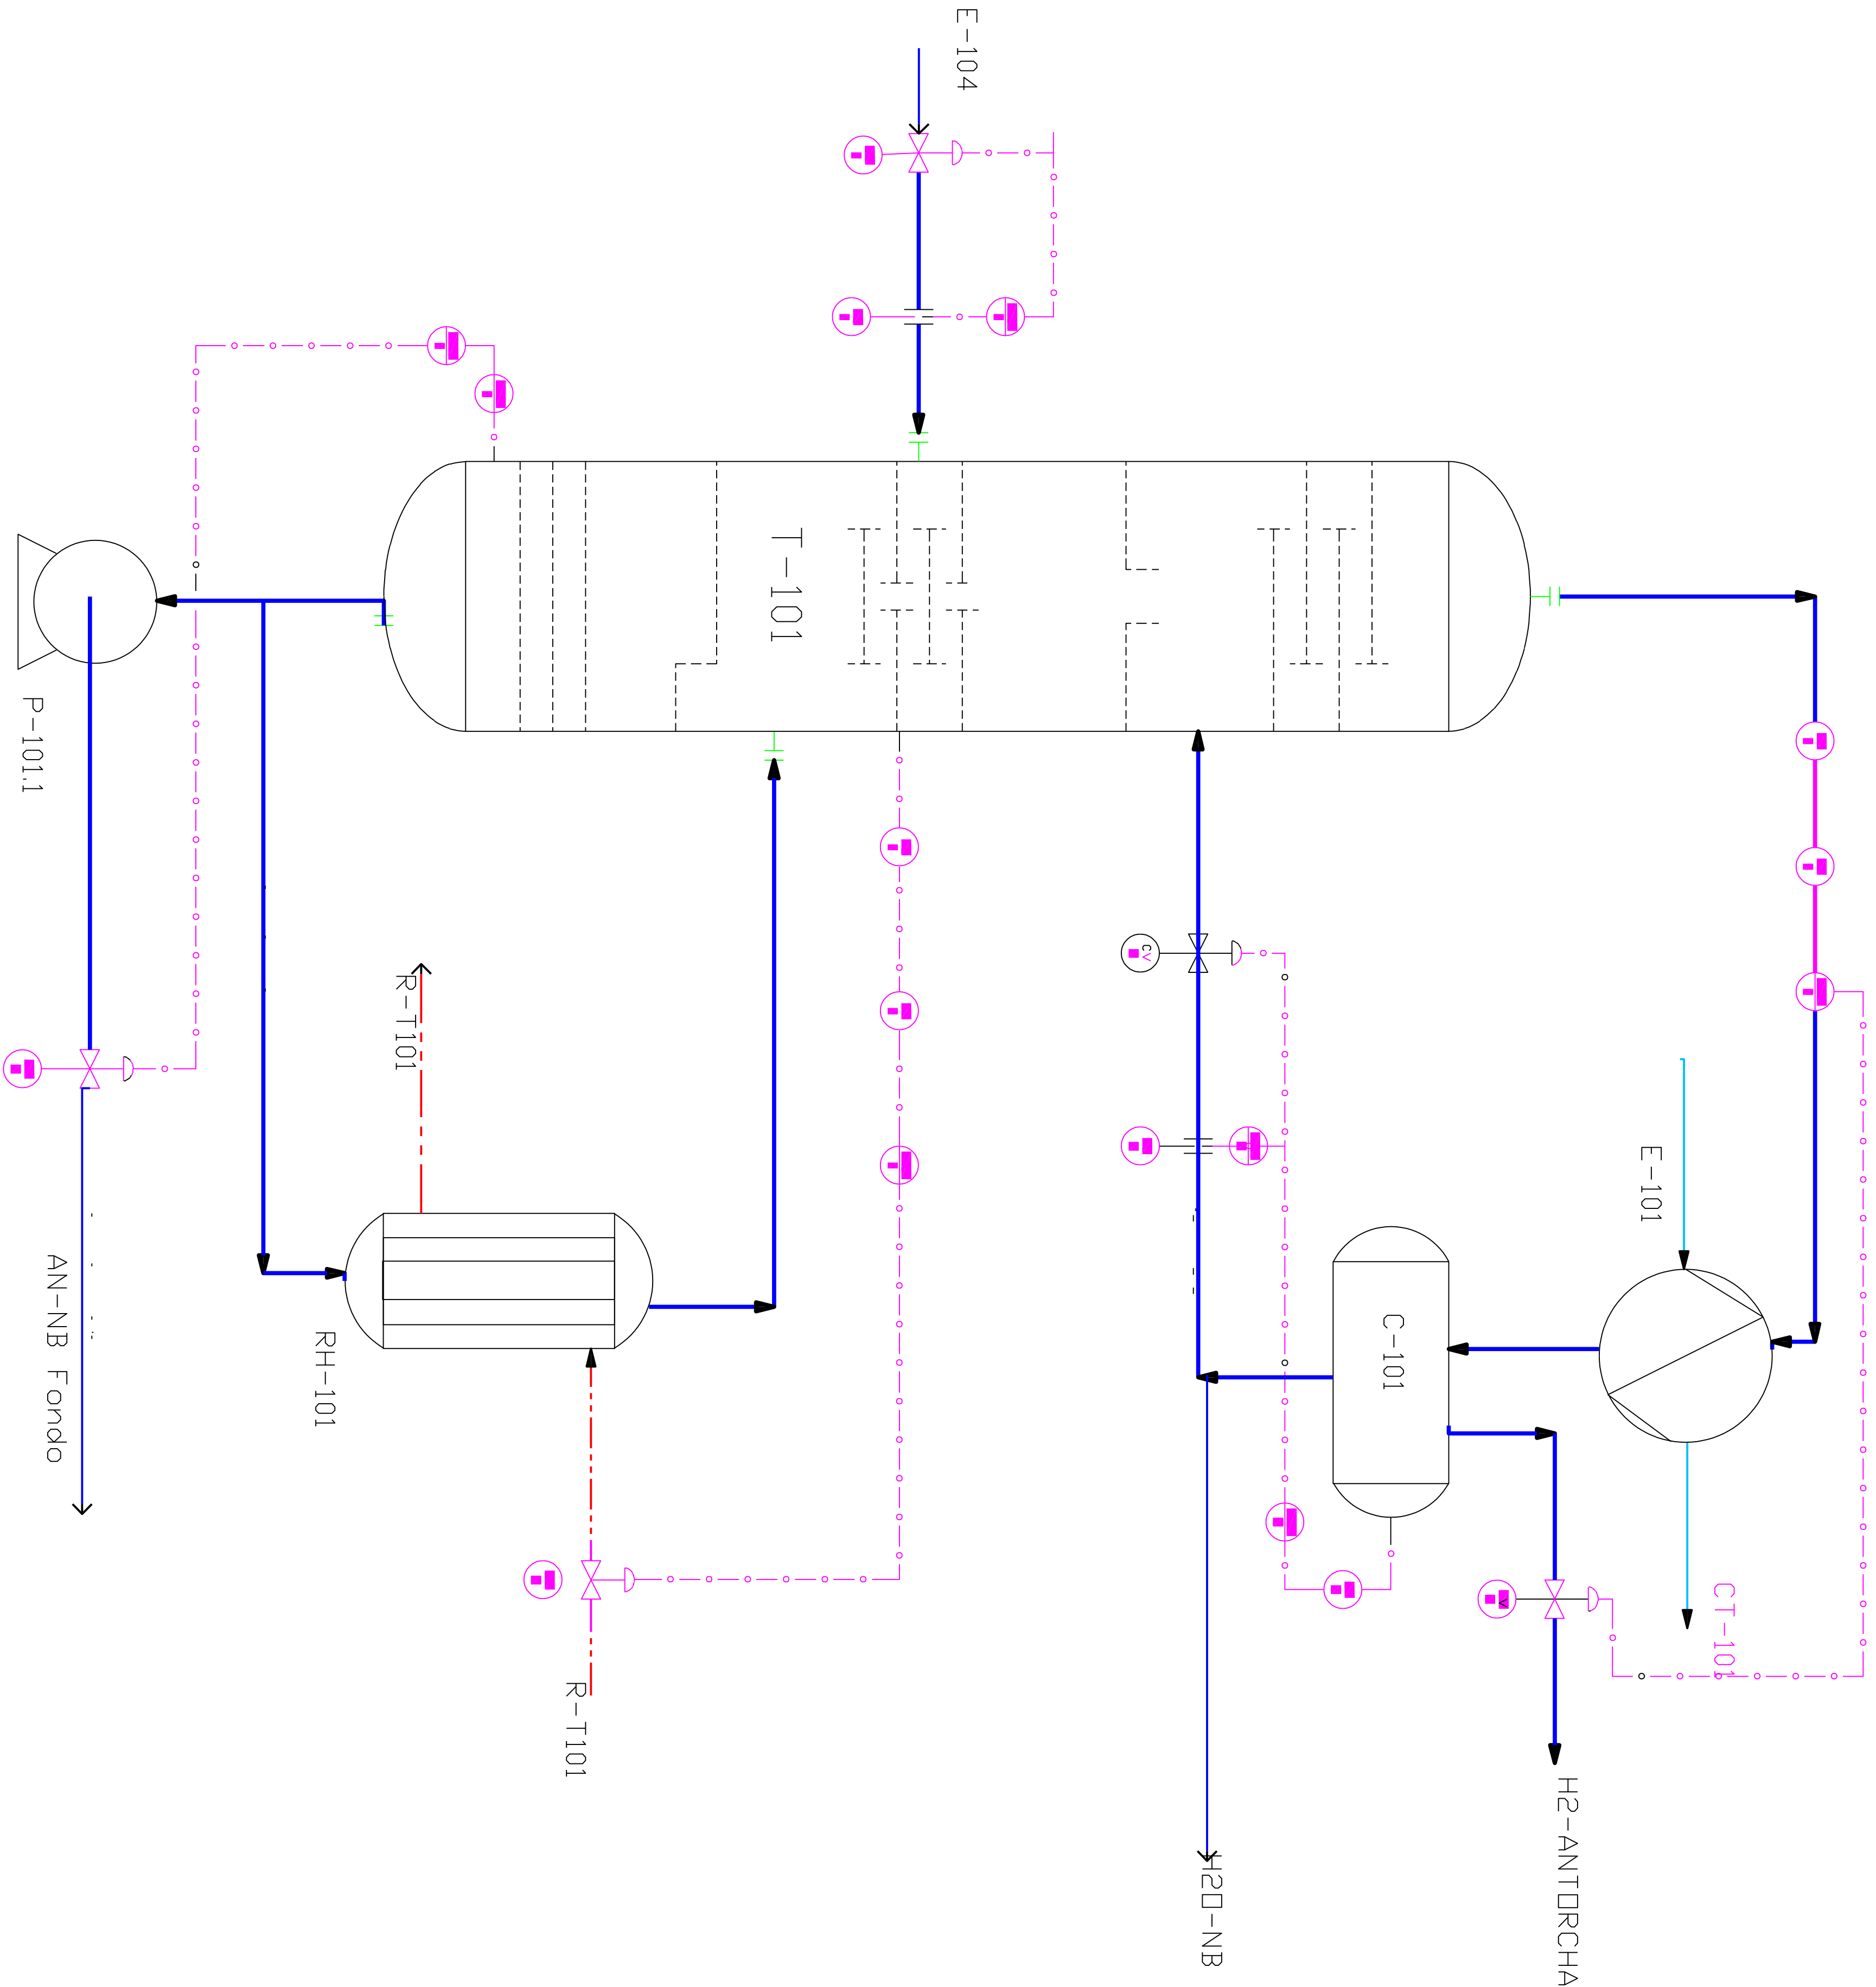

General Notes

- Rehervidor
- Columna de destilación
- Condensador parcial
- Tanque de destilado
- Válvula de control
- Transmisor de flujo
- Elemento de flujo
- Controlador de flujo
- Transmisor de presión
- Elemento de presión
- Controlador de presión
- Transmisor de temperatura
- Elemento de temperatura
- Controlador de temperatura

No.	Revision/Issue	Date

Columna de
destilación T101
###

Project Name and Address

ANILINA
Planta de Anilina

Area

###

Drawing Number

###

Author

C6H6_