



V-102: Separador de los productos del Domo de T-101

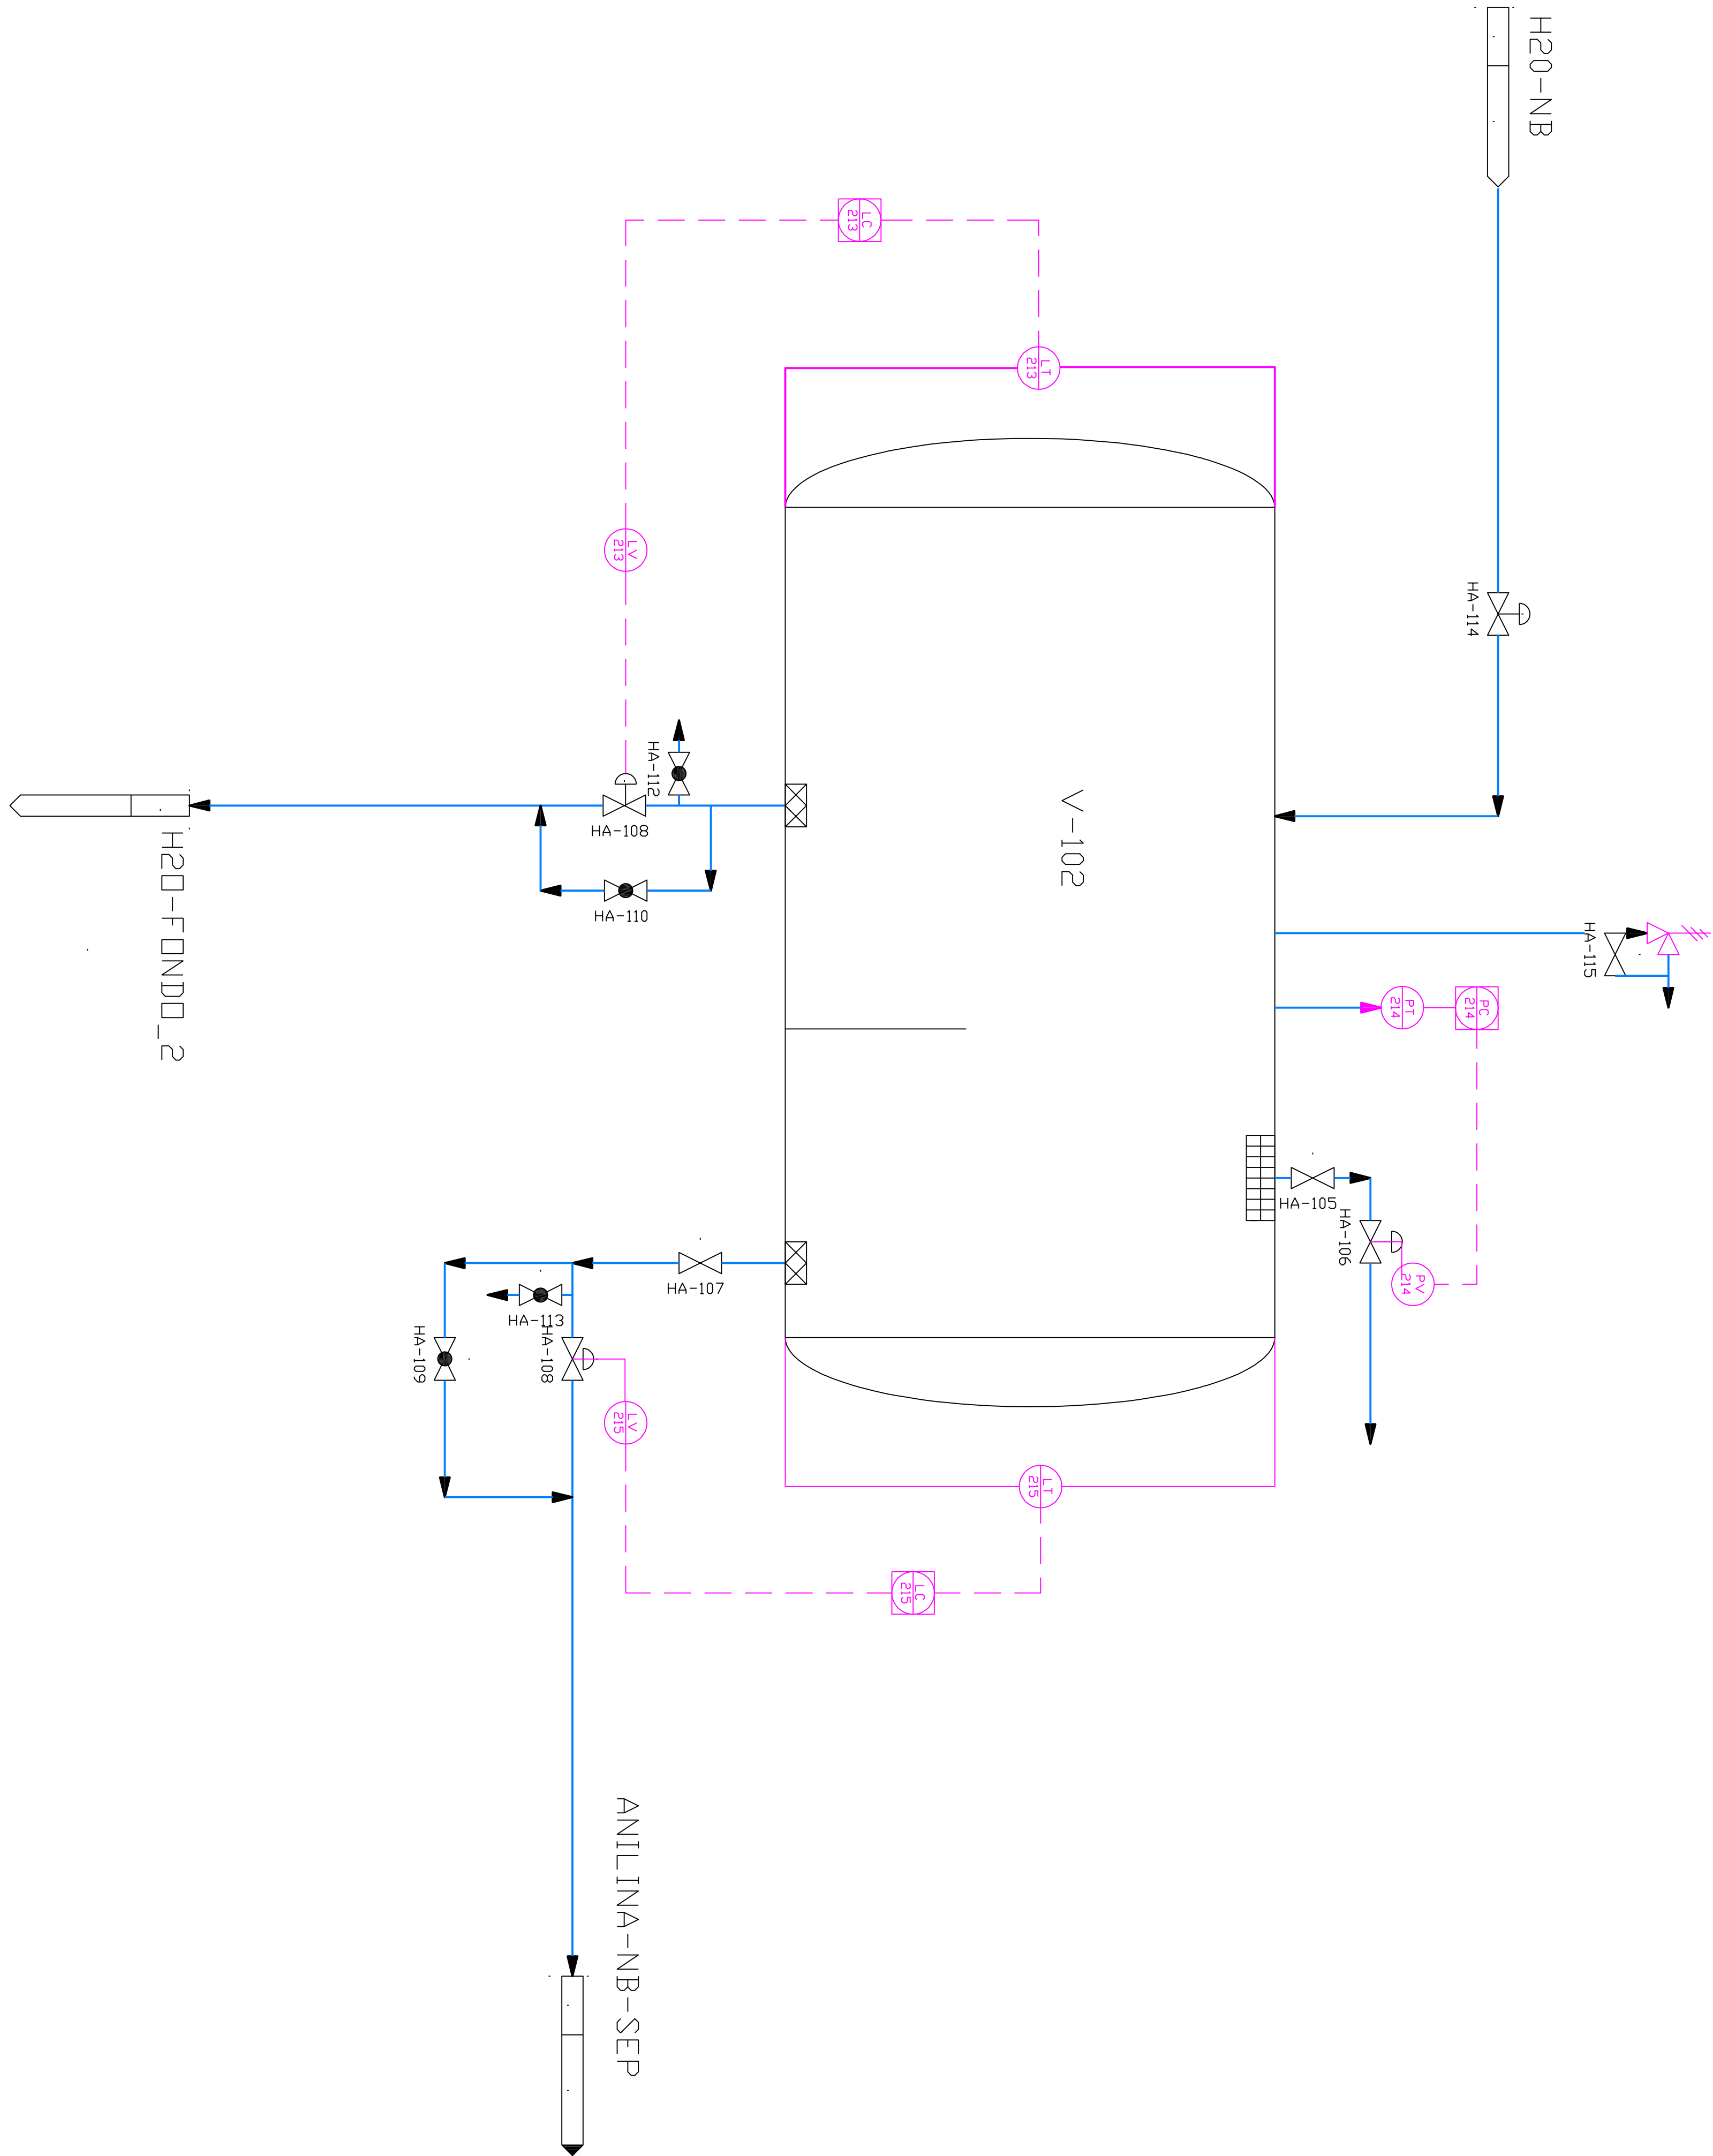

General Notes

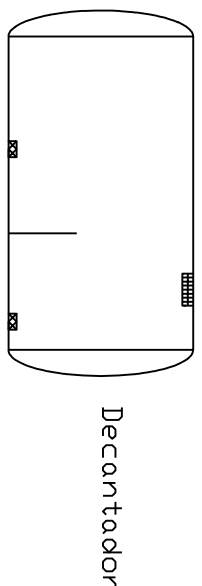

Válvula de alivio

Válvula de compuerta

Válvula de control

Transmisor de flujo

Elemento de flujo

Controlador de flujo

Transmisor de presión

Elemento de presión

Controlador de presión

Transmisor de temperatura

Elemento de temperatura

Controlador de temperatura

No.	Revision/Issue	Date

Drawing Name

Decantador V102

####

Project Name and Address

ANILINA

Planta de Anilina

Area	####	Stamp
Drawing Number	####	
Author	ESIOIE IPN	