


E-105: Enfriador de la primera columna de destilación
Coraza: Agua de enfriamiento
Tubos: Anilina Nitrobenceno

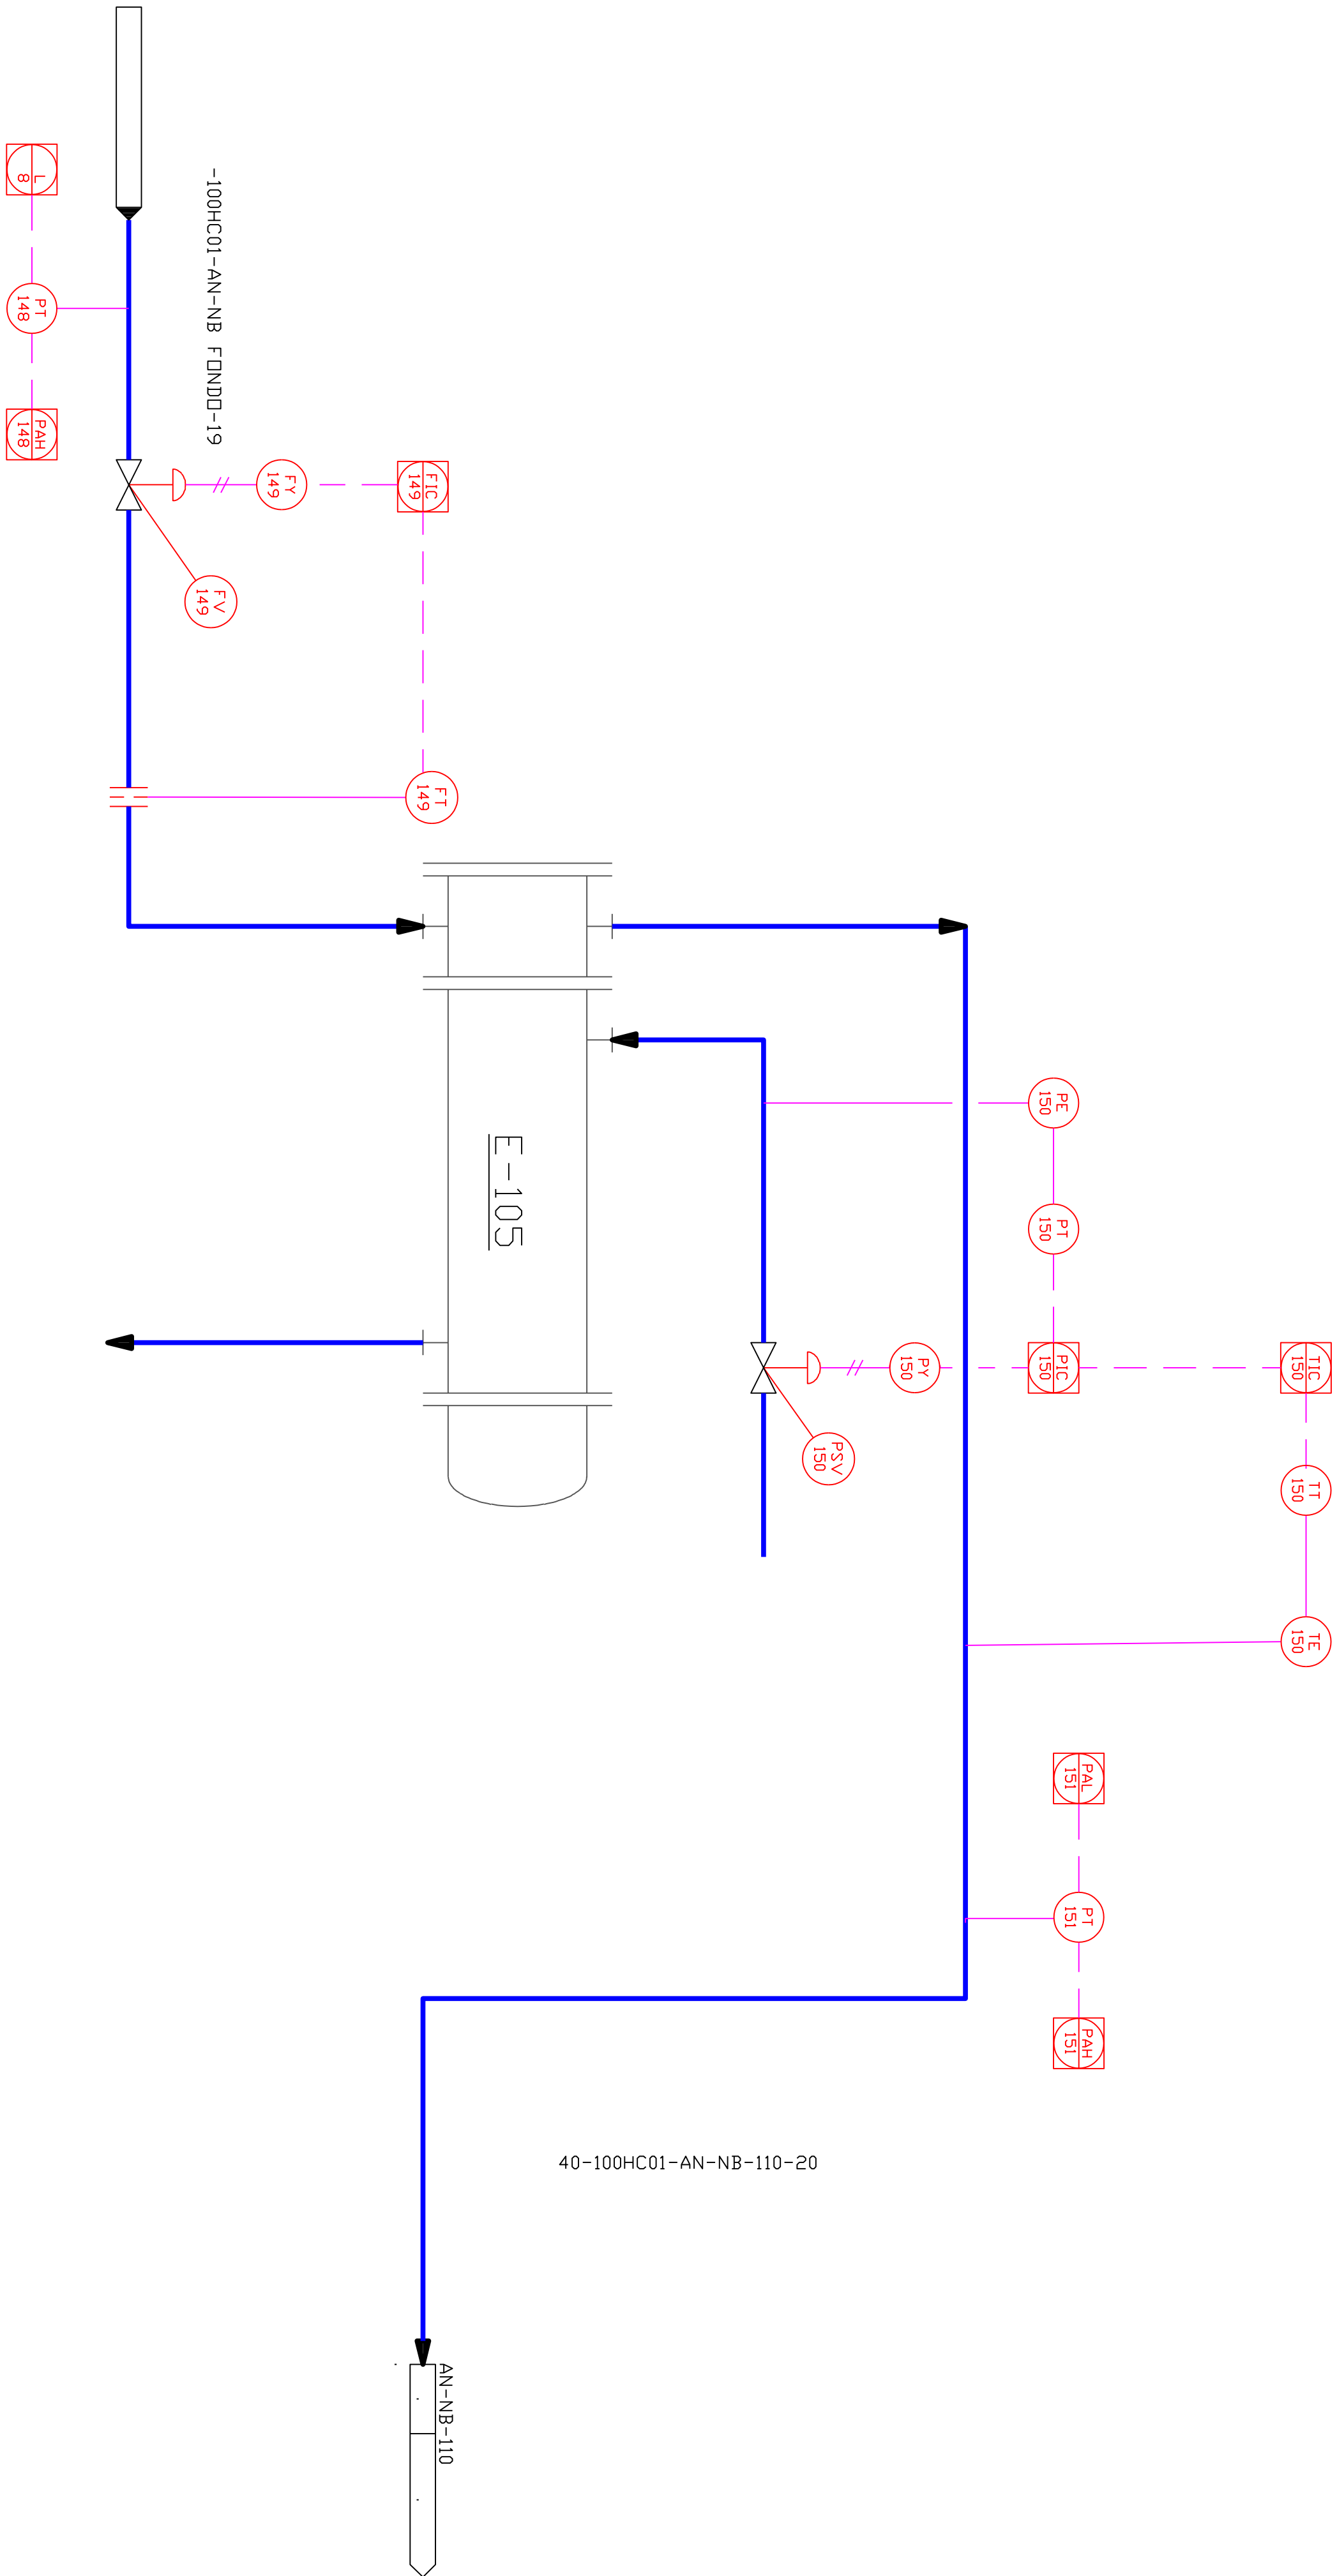

General Notes

- Valvula de control
- Intercambiador de calor
- TE Elemento de temperatura
- PAH Alarma de presión baja
- FIC Controlador indicador de flujo
- FV Convertidor de señal de flujo
- FT Transmisor de flujo
- PI Transmisor de presión
- PAH Alarma de presión alta
- PE Elemento de presión
- PIC Controlador indicador de presión
- FV Convertidor de señal de presión
- TIC Controlador indicador de temperatura
- TI Transmisor de temperatura

No.	Revision/Issue	Date

Enfriador primera
columna

Project Name and Address

ANILINA
Planta de Anilina

Area: ###

Drawing Number

###

Author

ESIQIE IPN