


H-100: Calentador de Hidrógeno

Coraza: Vapor de caldera

Tubos: Hidrógeno

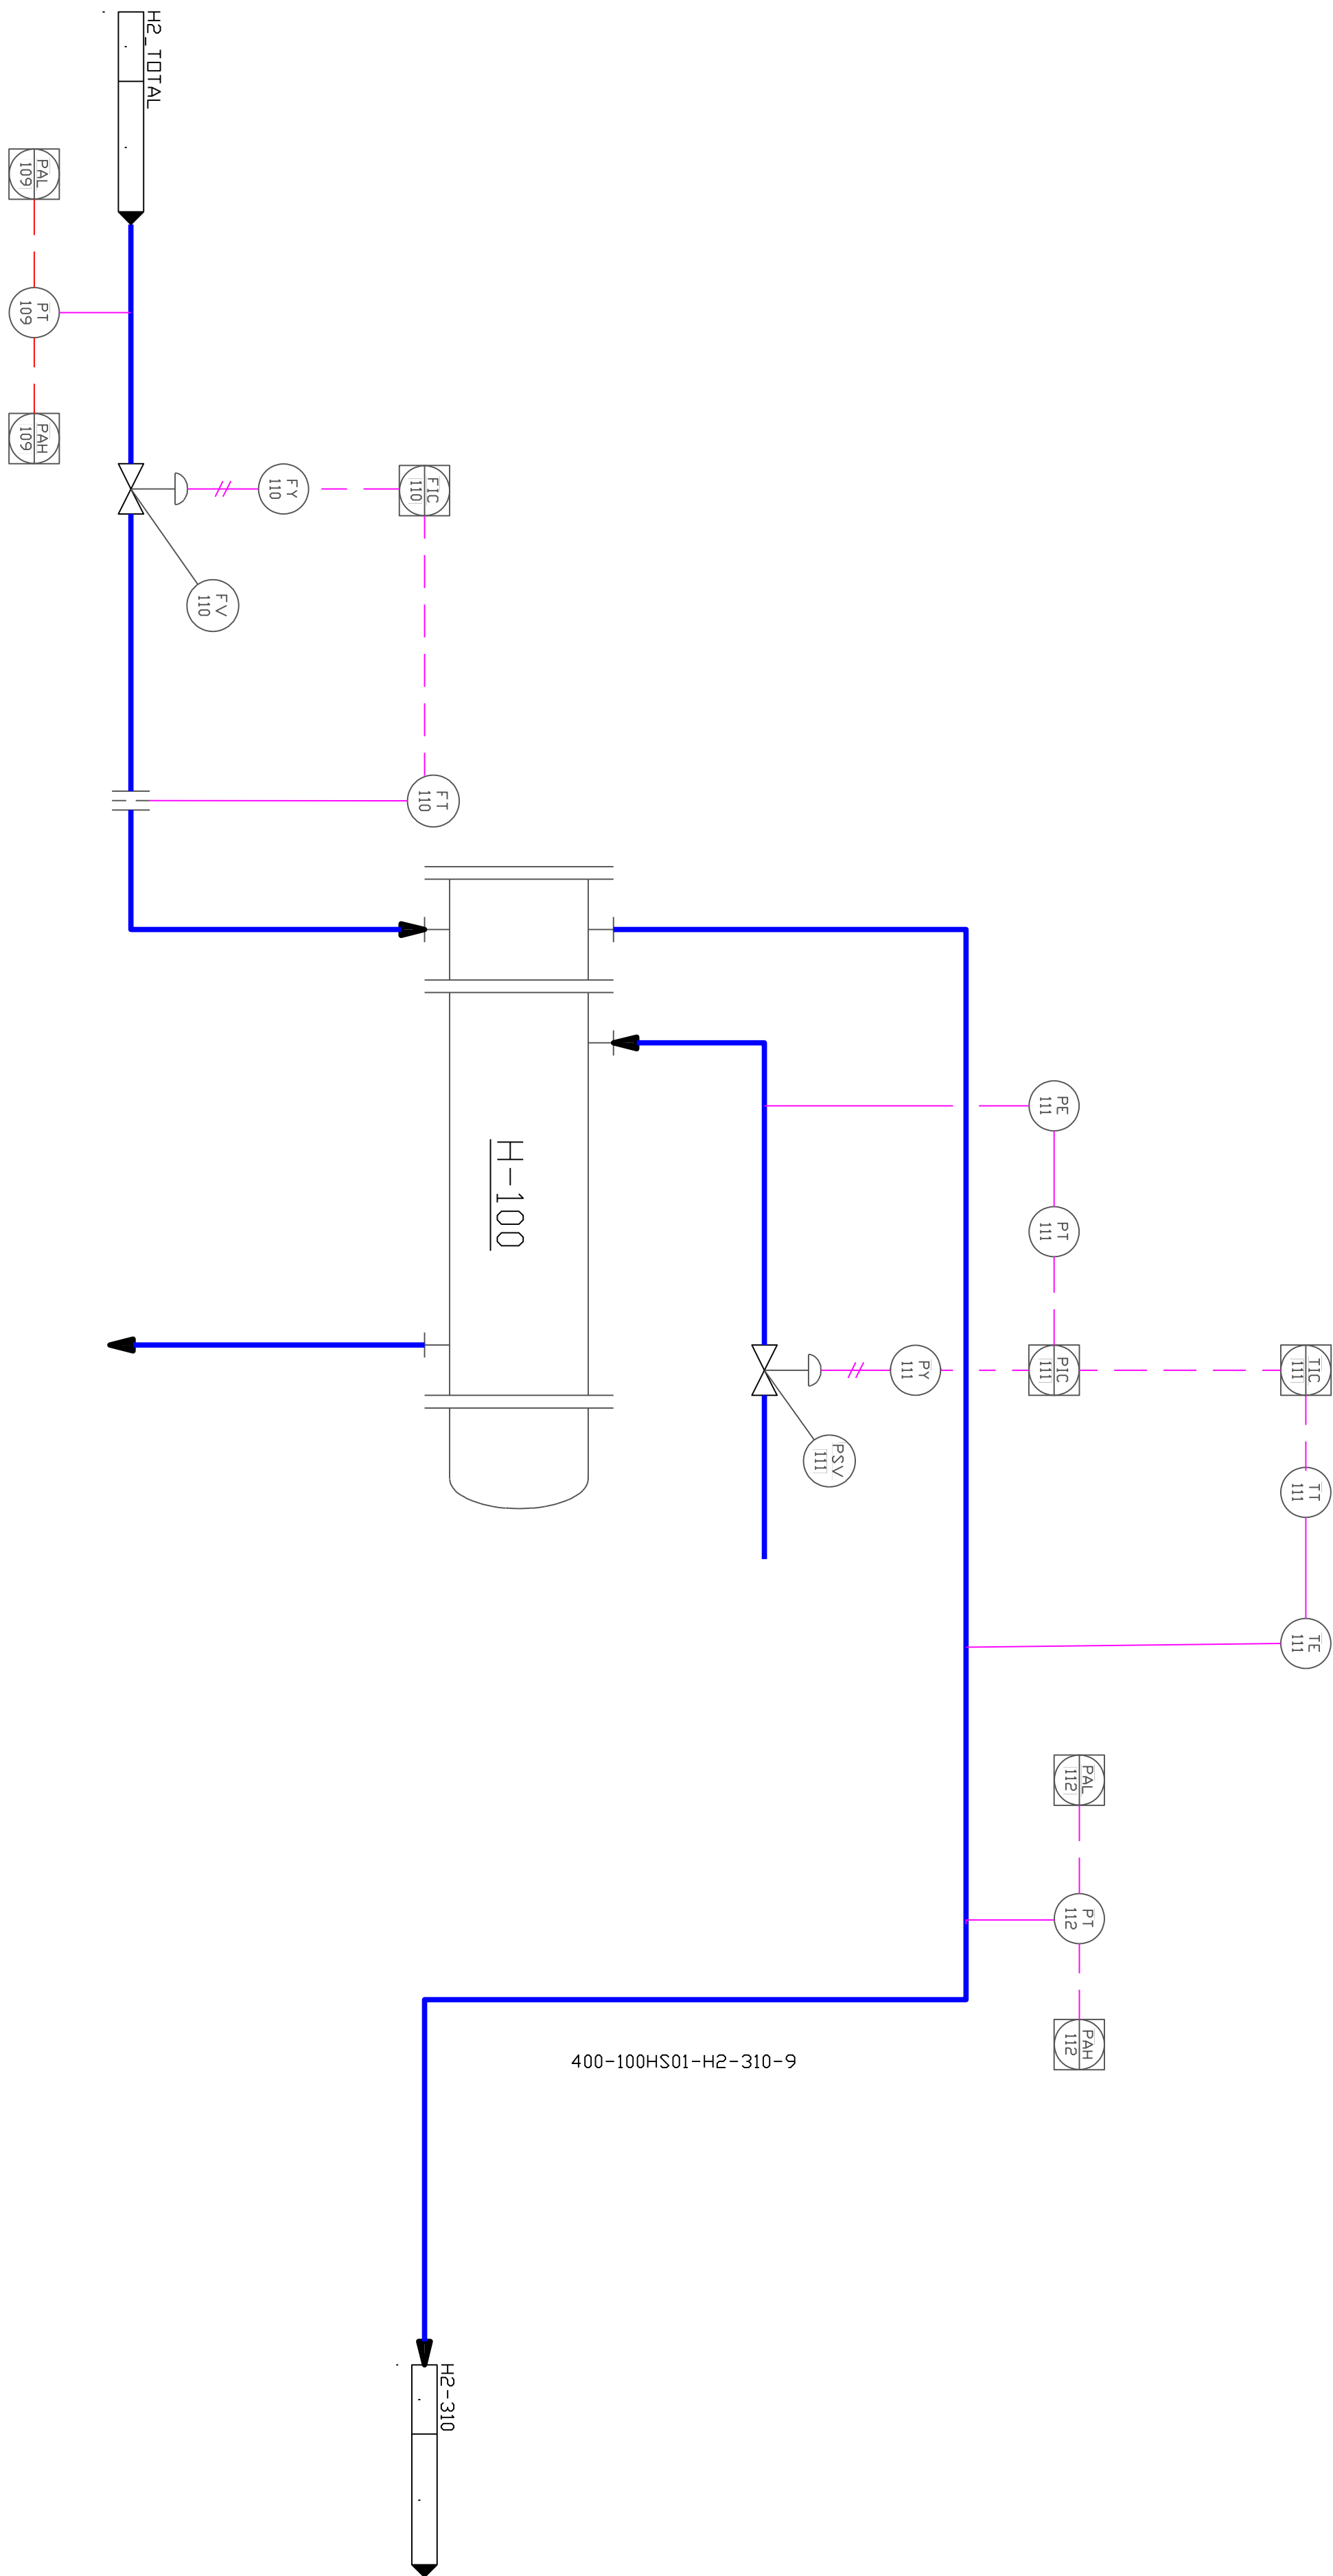

General Notes



- TE Elemento de temperatura
- PAH Alarma de presión baja
- FIC Controlador indicador de flujo
- FV Convertidor de señal de flujo
- FI Transmisor de flujo
- PI Transmisor de presión
- PAH Alarma de presión alta
- PE Alarma de presión alta
- PI Controlador indicador de presión
- FV Convertidor de señal de presión
- TIC Controlador indicador de temperatura
- TI Transmisor de temperatura

No.	Revision/Issue	Date

Drawing Name
Intercambiador de calor de H2

Project Name and Address
ANILINA
Planta de Anilina

Area	###	Stamp
Drawing Number	2	
Author	ESQIE	