


E-101: Primer enfriador despues de la reaccion
Coraza: Vapor de caldera
Tubos: Mezcla Hidrogeno-Nitrobenceno

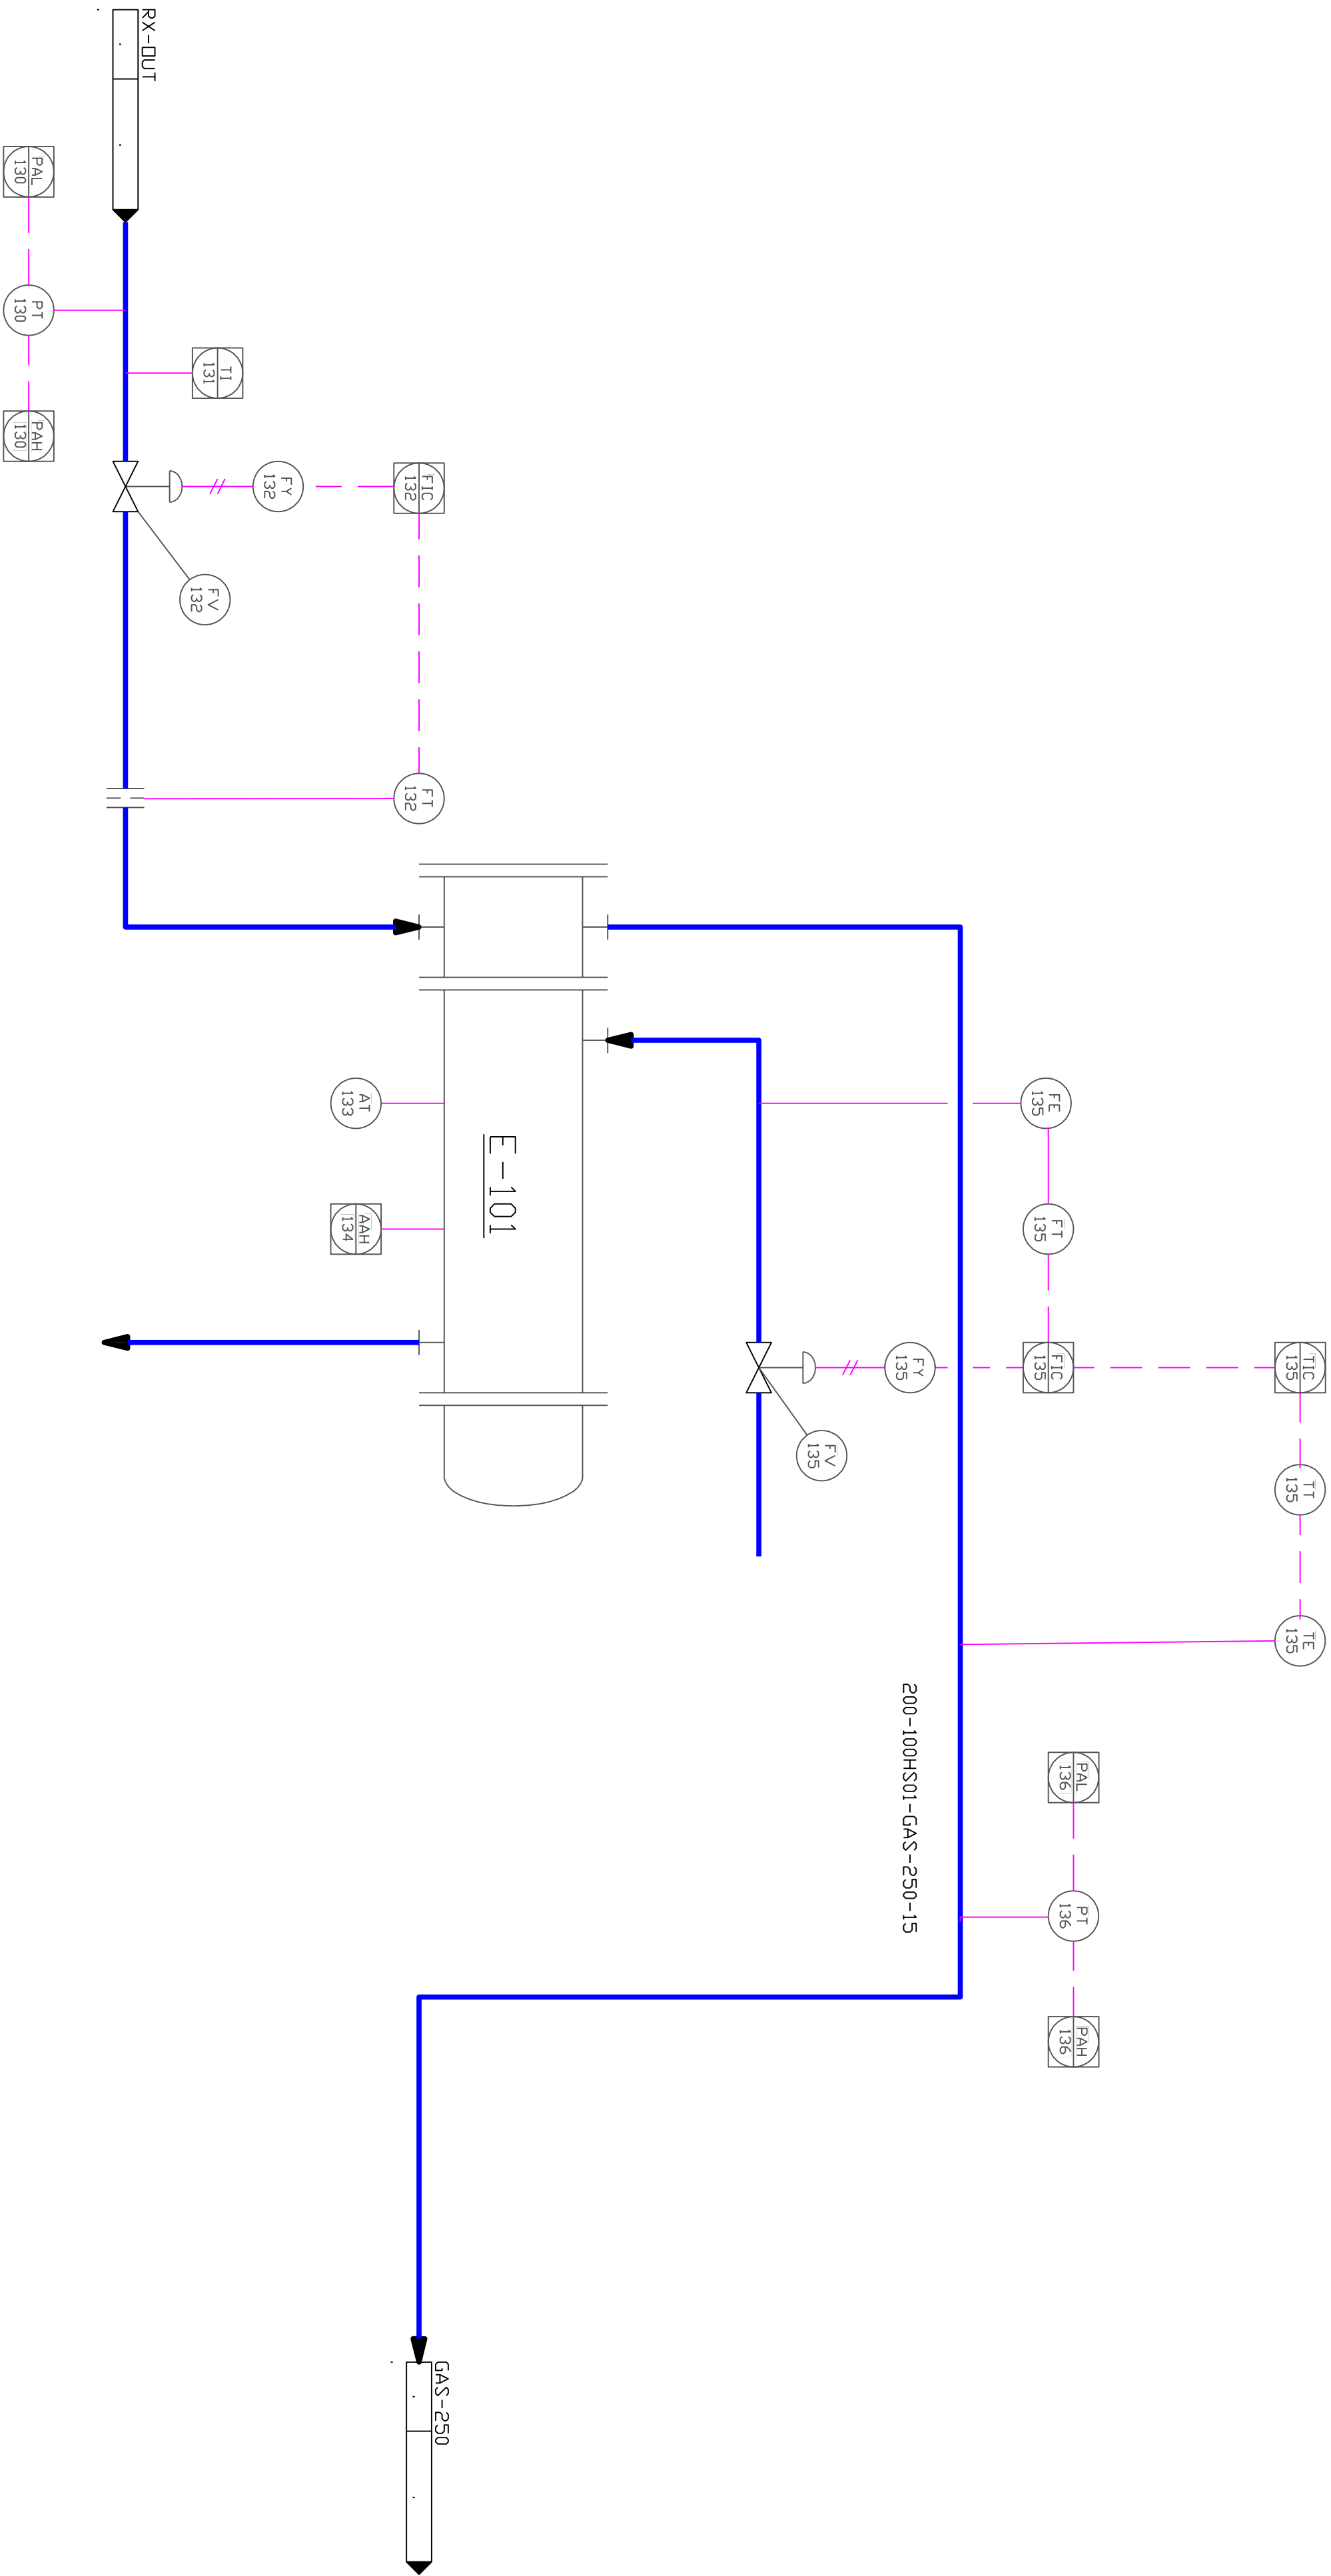

General Notes

Valvula de control

Intercambiador de calor

Elemento de temperatura

Alarma de presión baja

Controlador indicador de flujo

Convertidor de señal de flujo

Transmisor de flujo

Transmisor de presión

Alarma de presión alta

Elemento de presión

Controlador indicador de presión

Convertidor de señal de presión

Controlador indicador de temperatura

Transmisor de temperatura

No.	Revision/Issue	Date

Intercambiador
despues del
reactor

Project Name and Address

ANILINA
Planta de Anilina

Area: ###

Drawing Number: ###

Author

ESIQIE IPN