




E-100: Calentador de Nitrobenceno
Cora za: Vapor de caldera
Tubos: Nitrobenceno

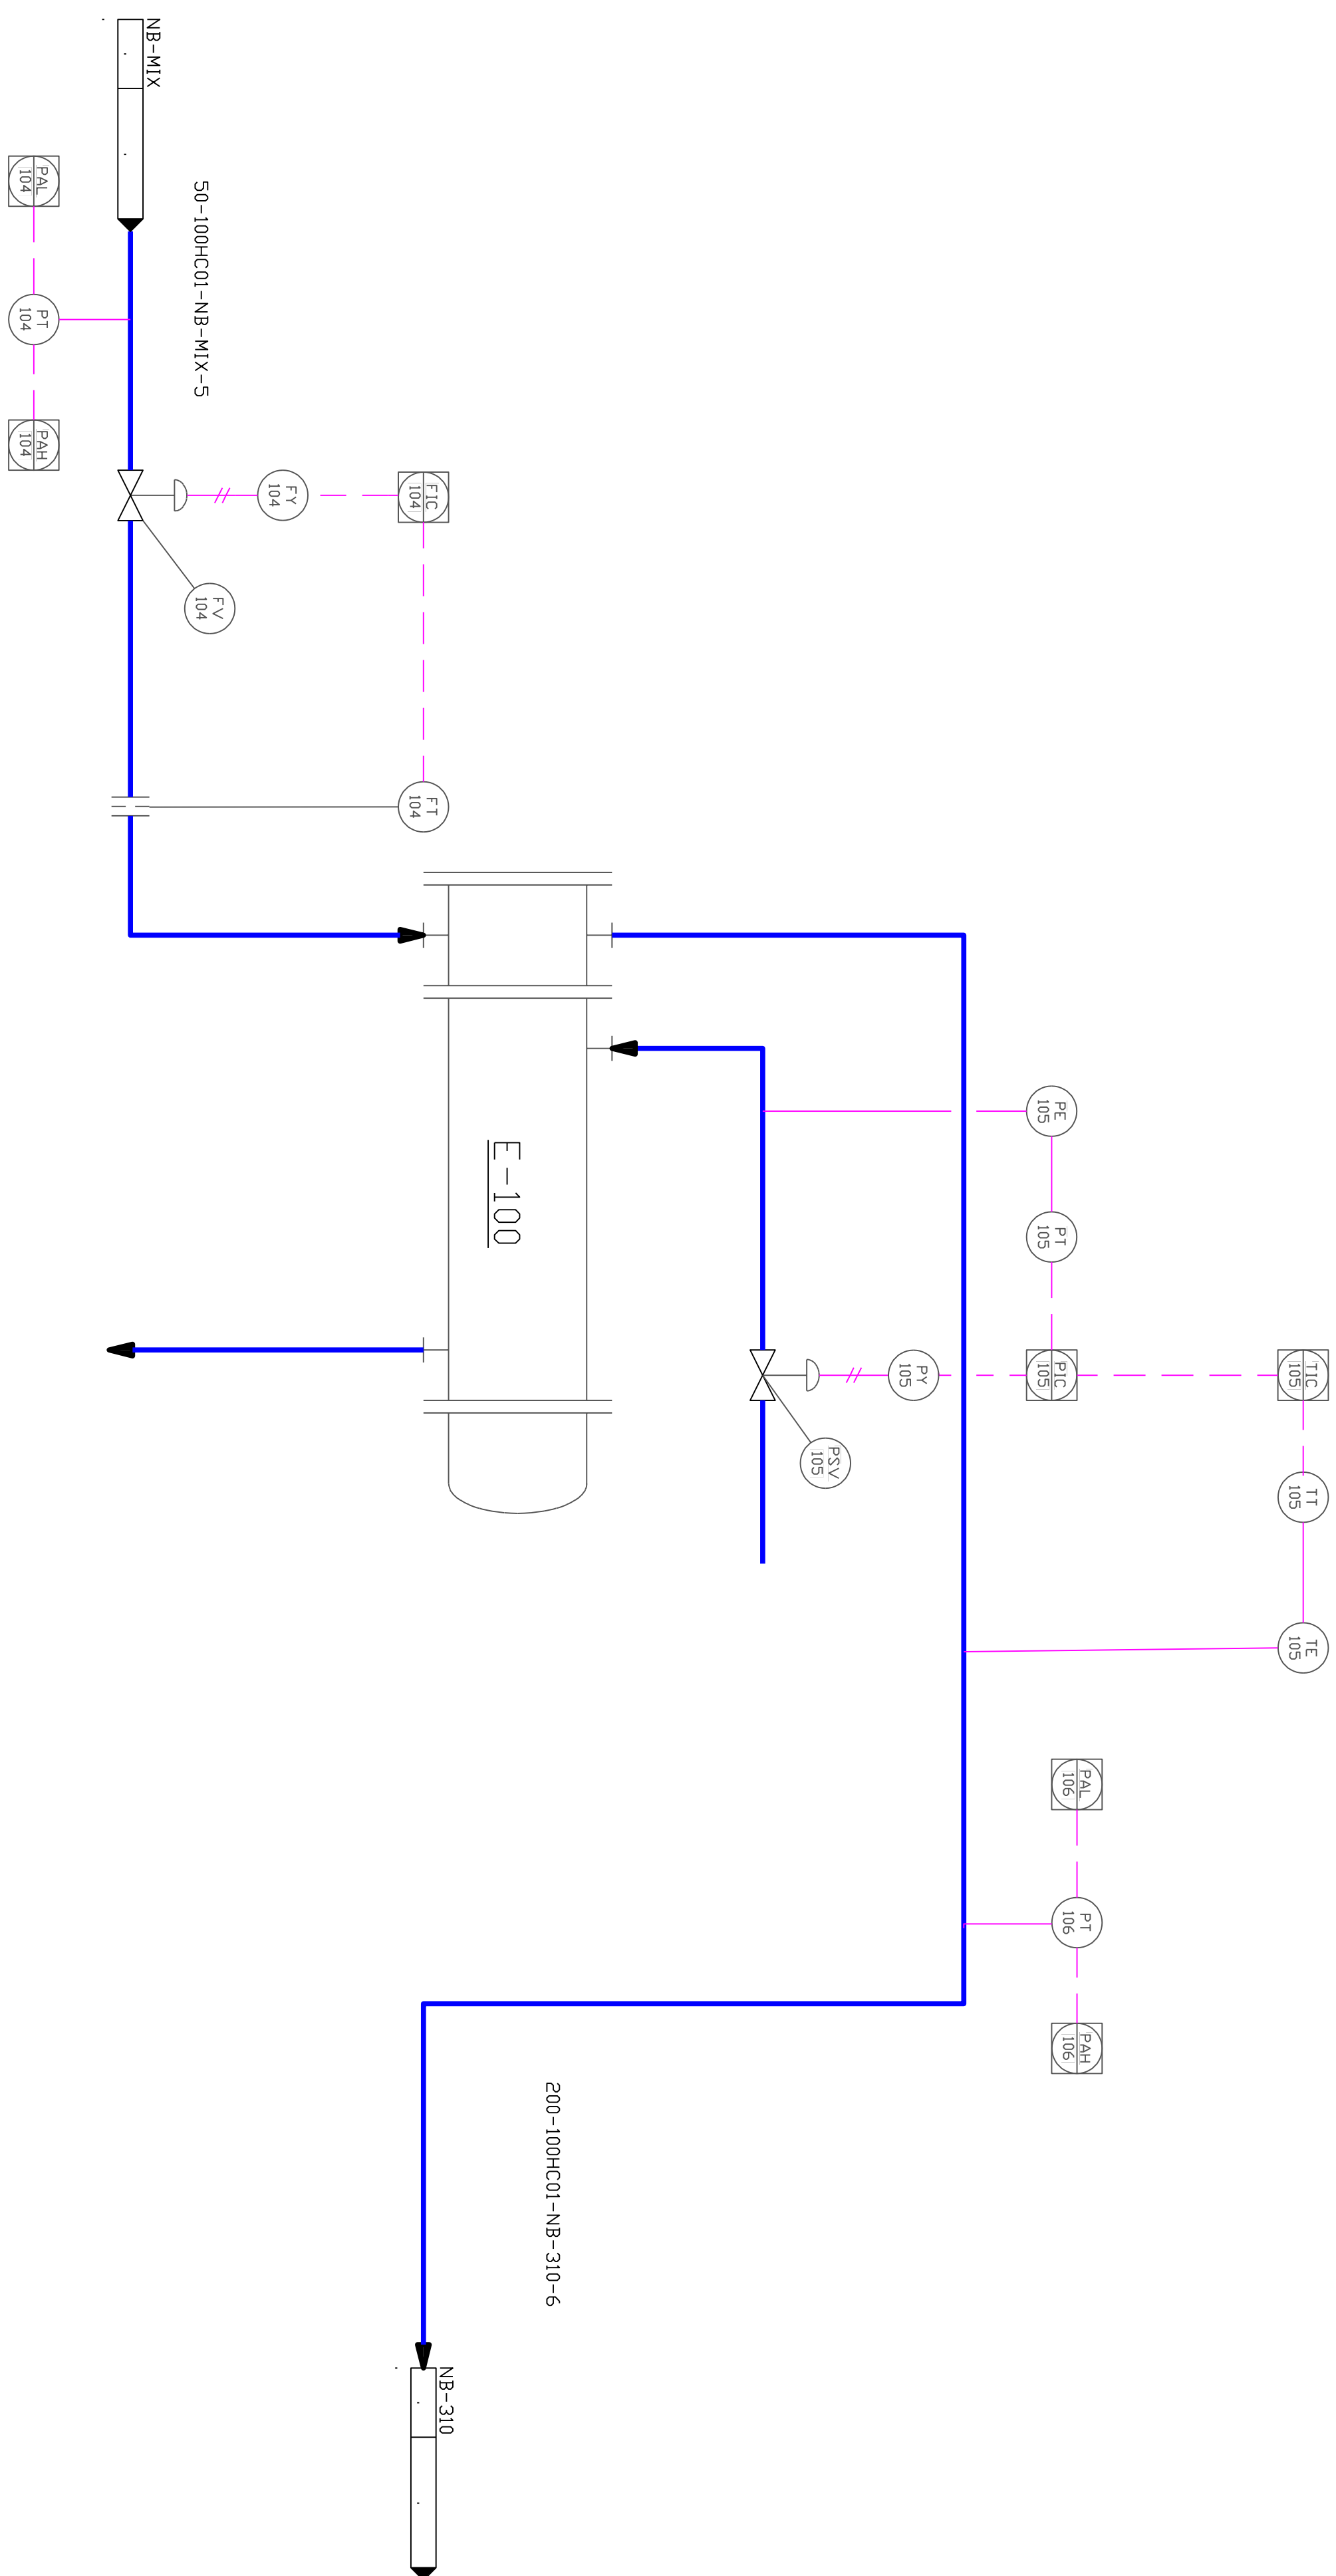


General Notes

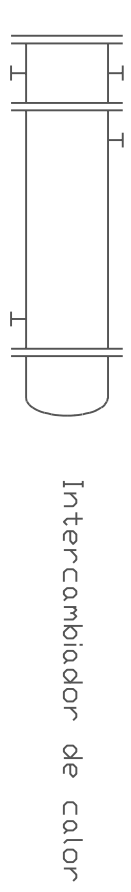

Intercambiador de calor

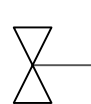

Valvula de control

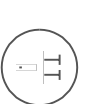

Transmisor de temperatura



Elemento de temperatura



Controlador indicador de temperatura



Controlador indicador de presión



Elemento de presión



Controlador indicado



Convertidor de señal de flujo



Alarma de presión alta



Transmisor de presión

No.	Revision/Issue	Date

Drawing Name

Intercambiador de Nitrobenceno

Project Name and Address

ANILINA

Planta de Anilina

—

Area	Stamp
#####	
Drawing Number	
#####	
Author	ESIQIE IPN