


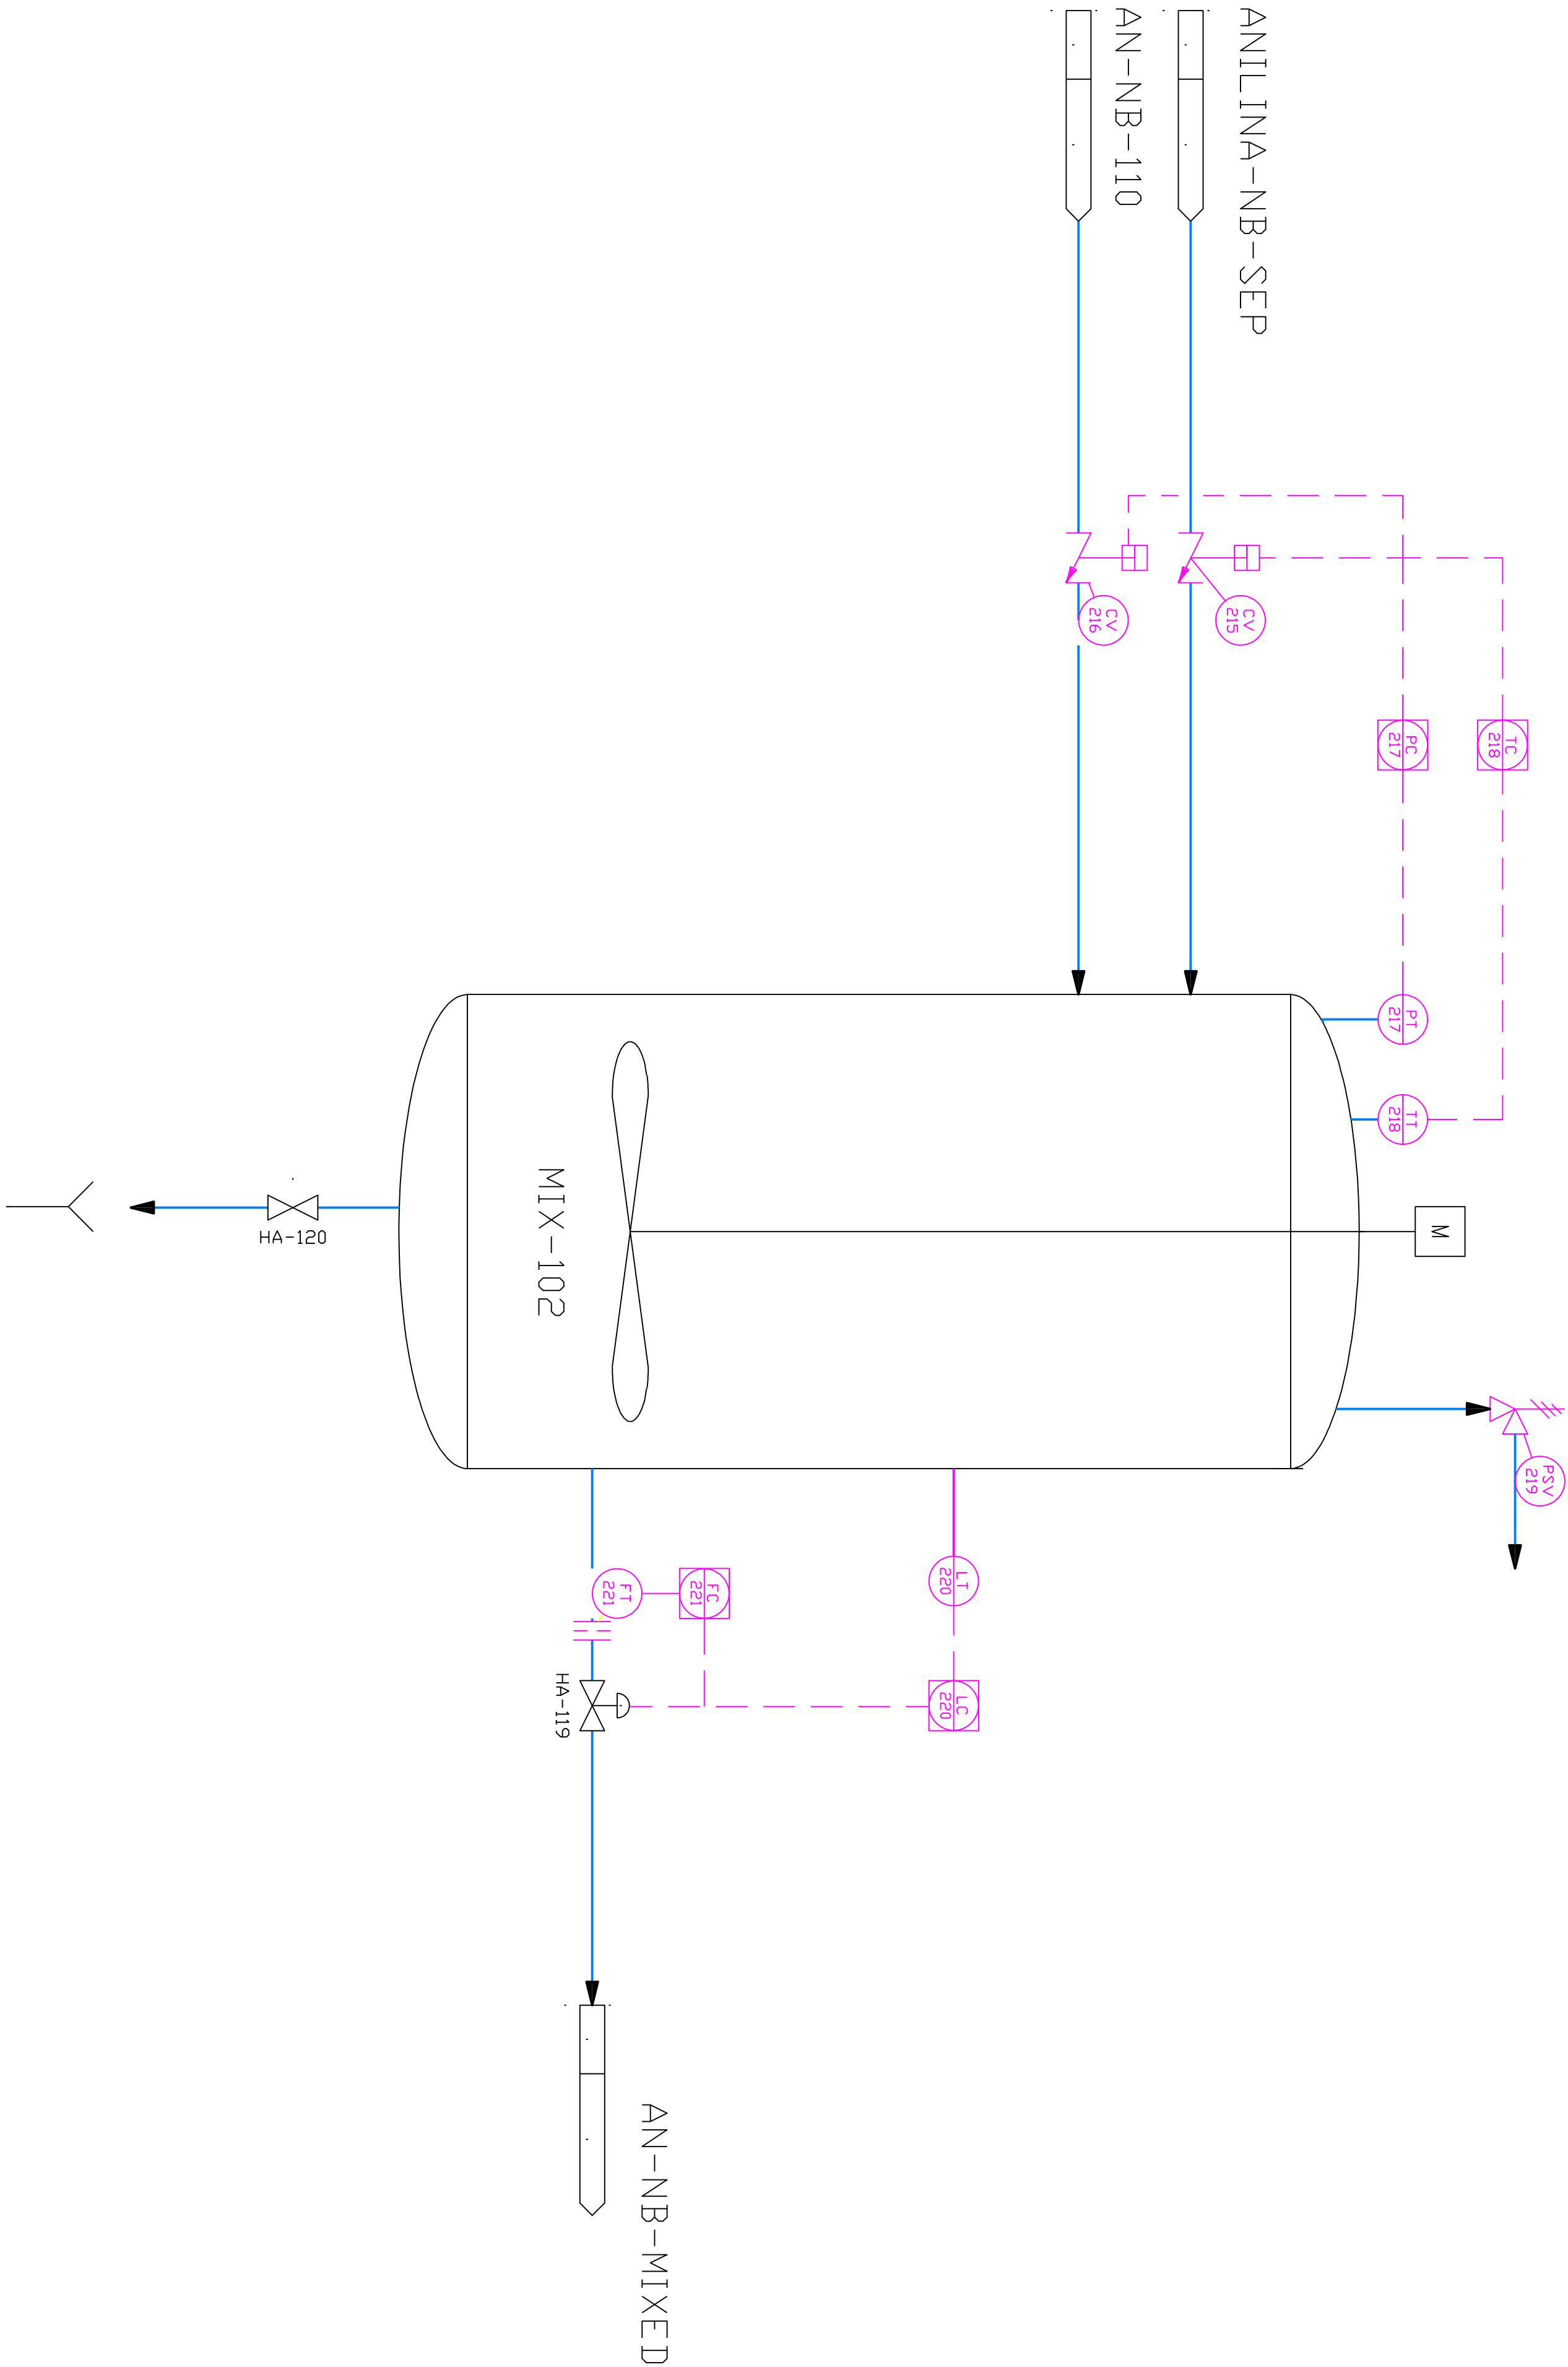

General Notes		
Drenaje		
Tanque mezclador		
Transmisor de flujo		
Controlador de flujo		
Transmisor de nivel		
Controlador de nivel		
Transmisor de temperatura		
Controlador de temperatura		
Transmisor de presión		
Controlador de presión		
No.	Revision/Issue	Date

Drawing Name	
MIXER102	
####	

Project Name and Address	
ANILINA	
Planta de Anilina	

Area	###	Stamp
Drawing Number	###	
Author	ESIOE IPN	