R-001: Reactor enchaquetado

340 Celcius

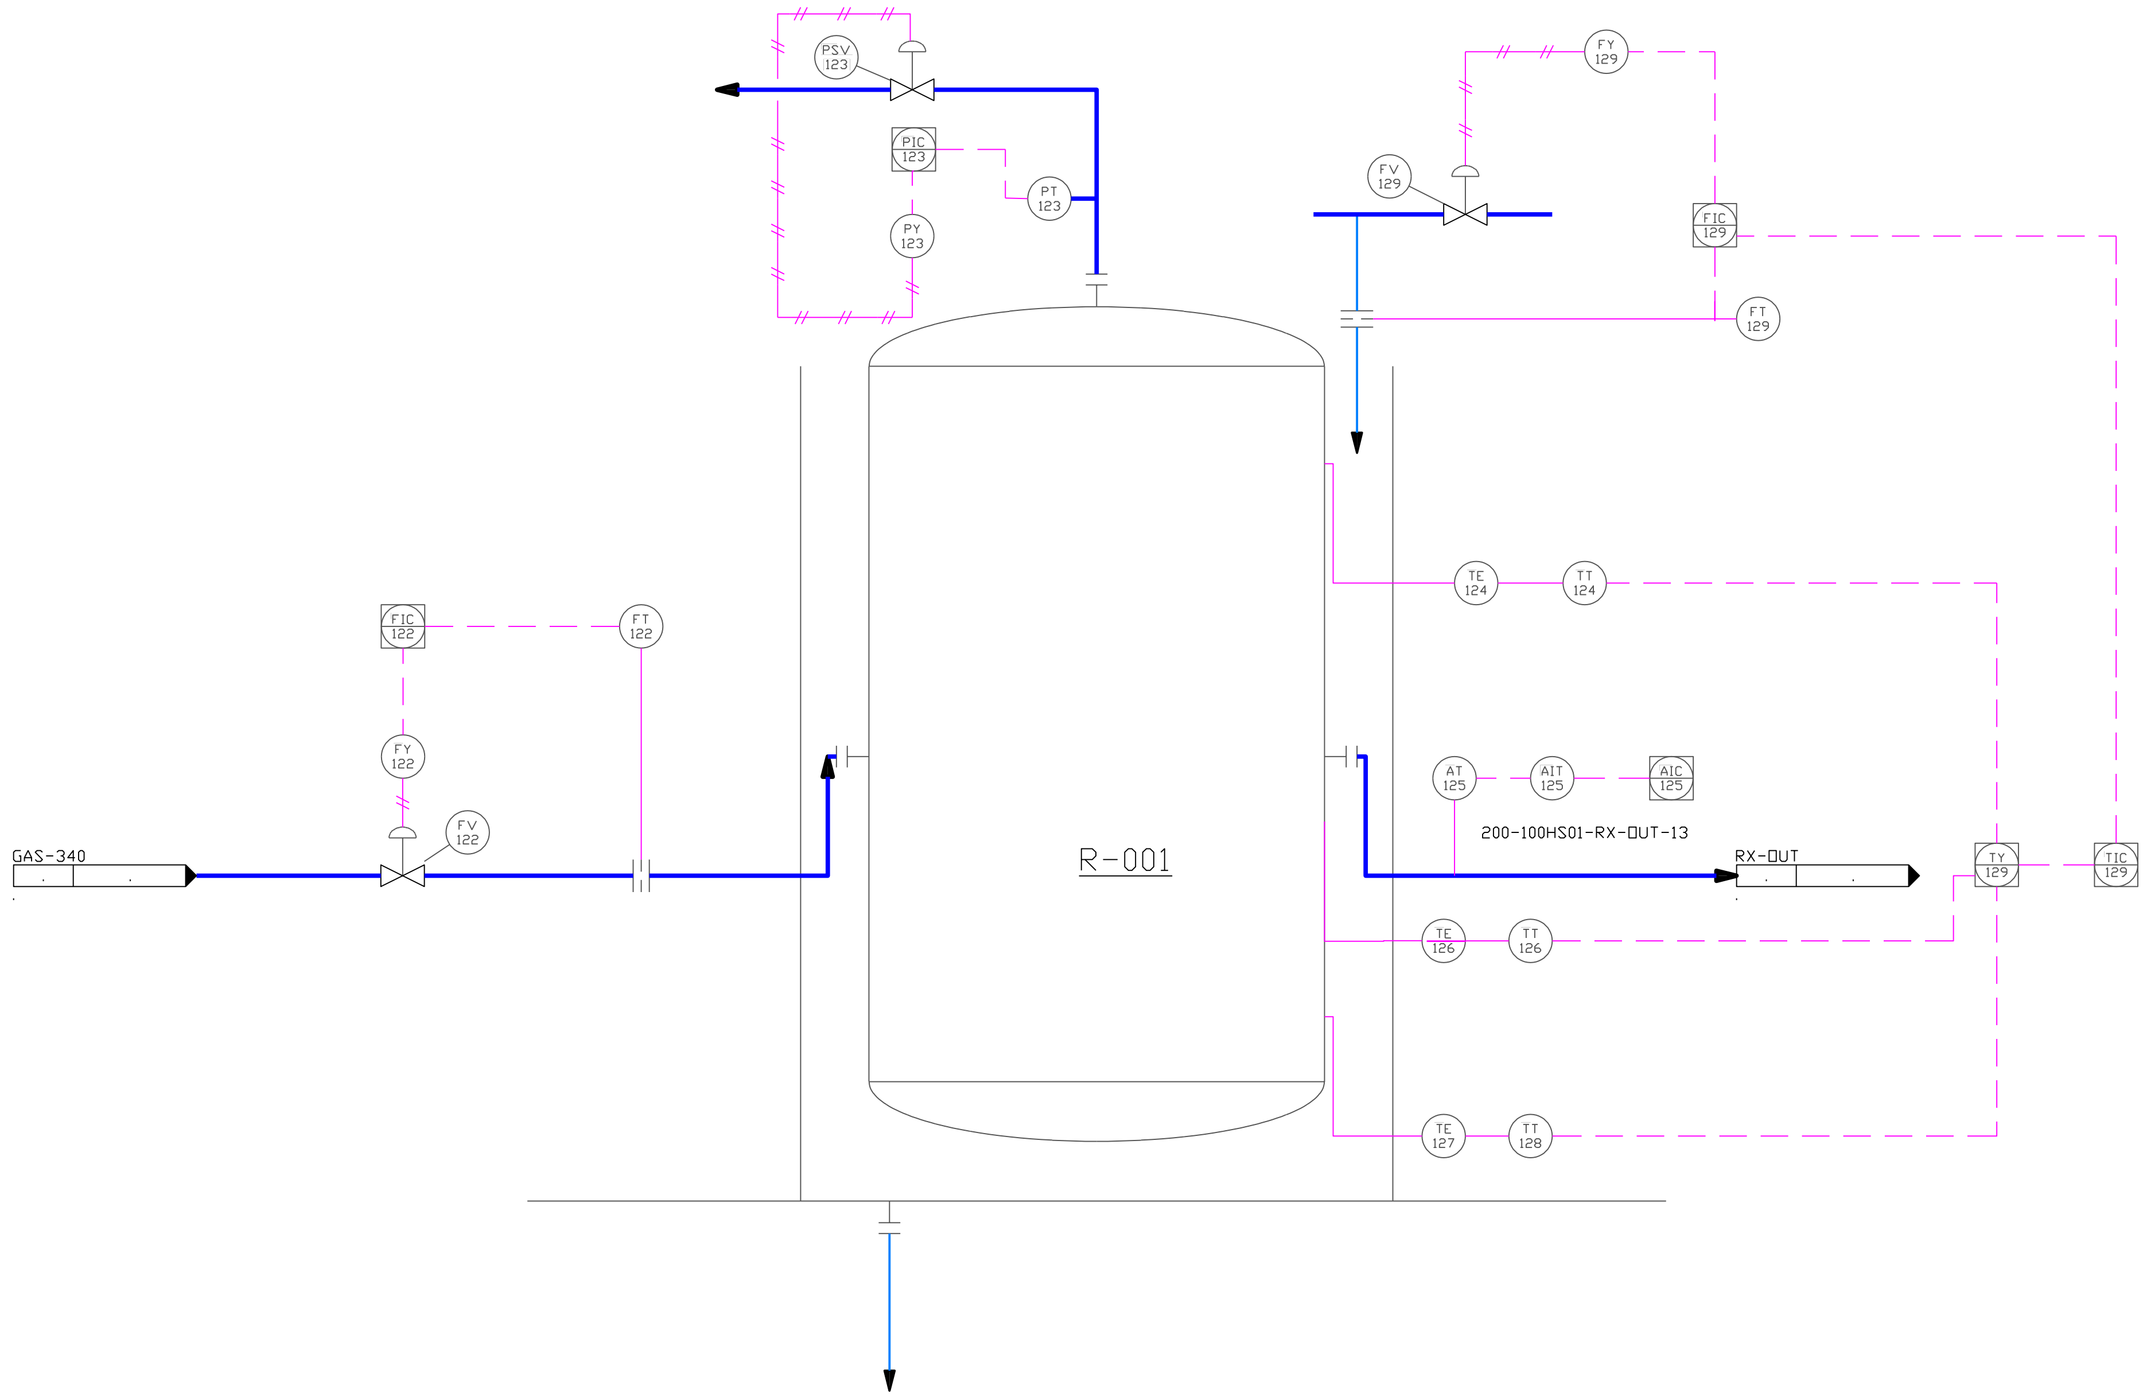

General Notes

Tanque enchaquetado

Valvula de control

TIC — Controlador indicadorl de temperatura

TY — Convertidor de señal de temperatura

AIC — Controlador indicador de analito

AIT — Transmisor indicador de analito

FIC — Controlador indicador de flujo

FT — Transmisor de flujo

FY — Convertidor de señal de flujo

PIC — Controlador indicador de presión

PY — Convertidor de señal de presión

PT — Transmisor de presión

TE — Elemento de temperatura

TT — Transmisor de temperatura

AT — Transmisor de analito

No.	Revision/Issue	Date

Drawing Name

Reactor Enchaquetado

Project Name and Address

ANILINA
Planta de Anilina

---- ----

Area	Stamp
####	
Drawing Number	
####	
Author	
ESIQIE IPN	

C:\Users\C6H6_\OneDrive\Documentos\ANILINA\PID DWG\reactor enchaquetado.dwg