


E-103: Segundo enfriador despues de la reacción
CoraZa: Agua de enfriamiento
Tubos:Mezcla hidrógeno-Nitrobenceno

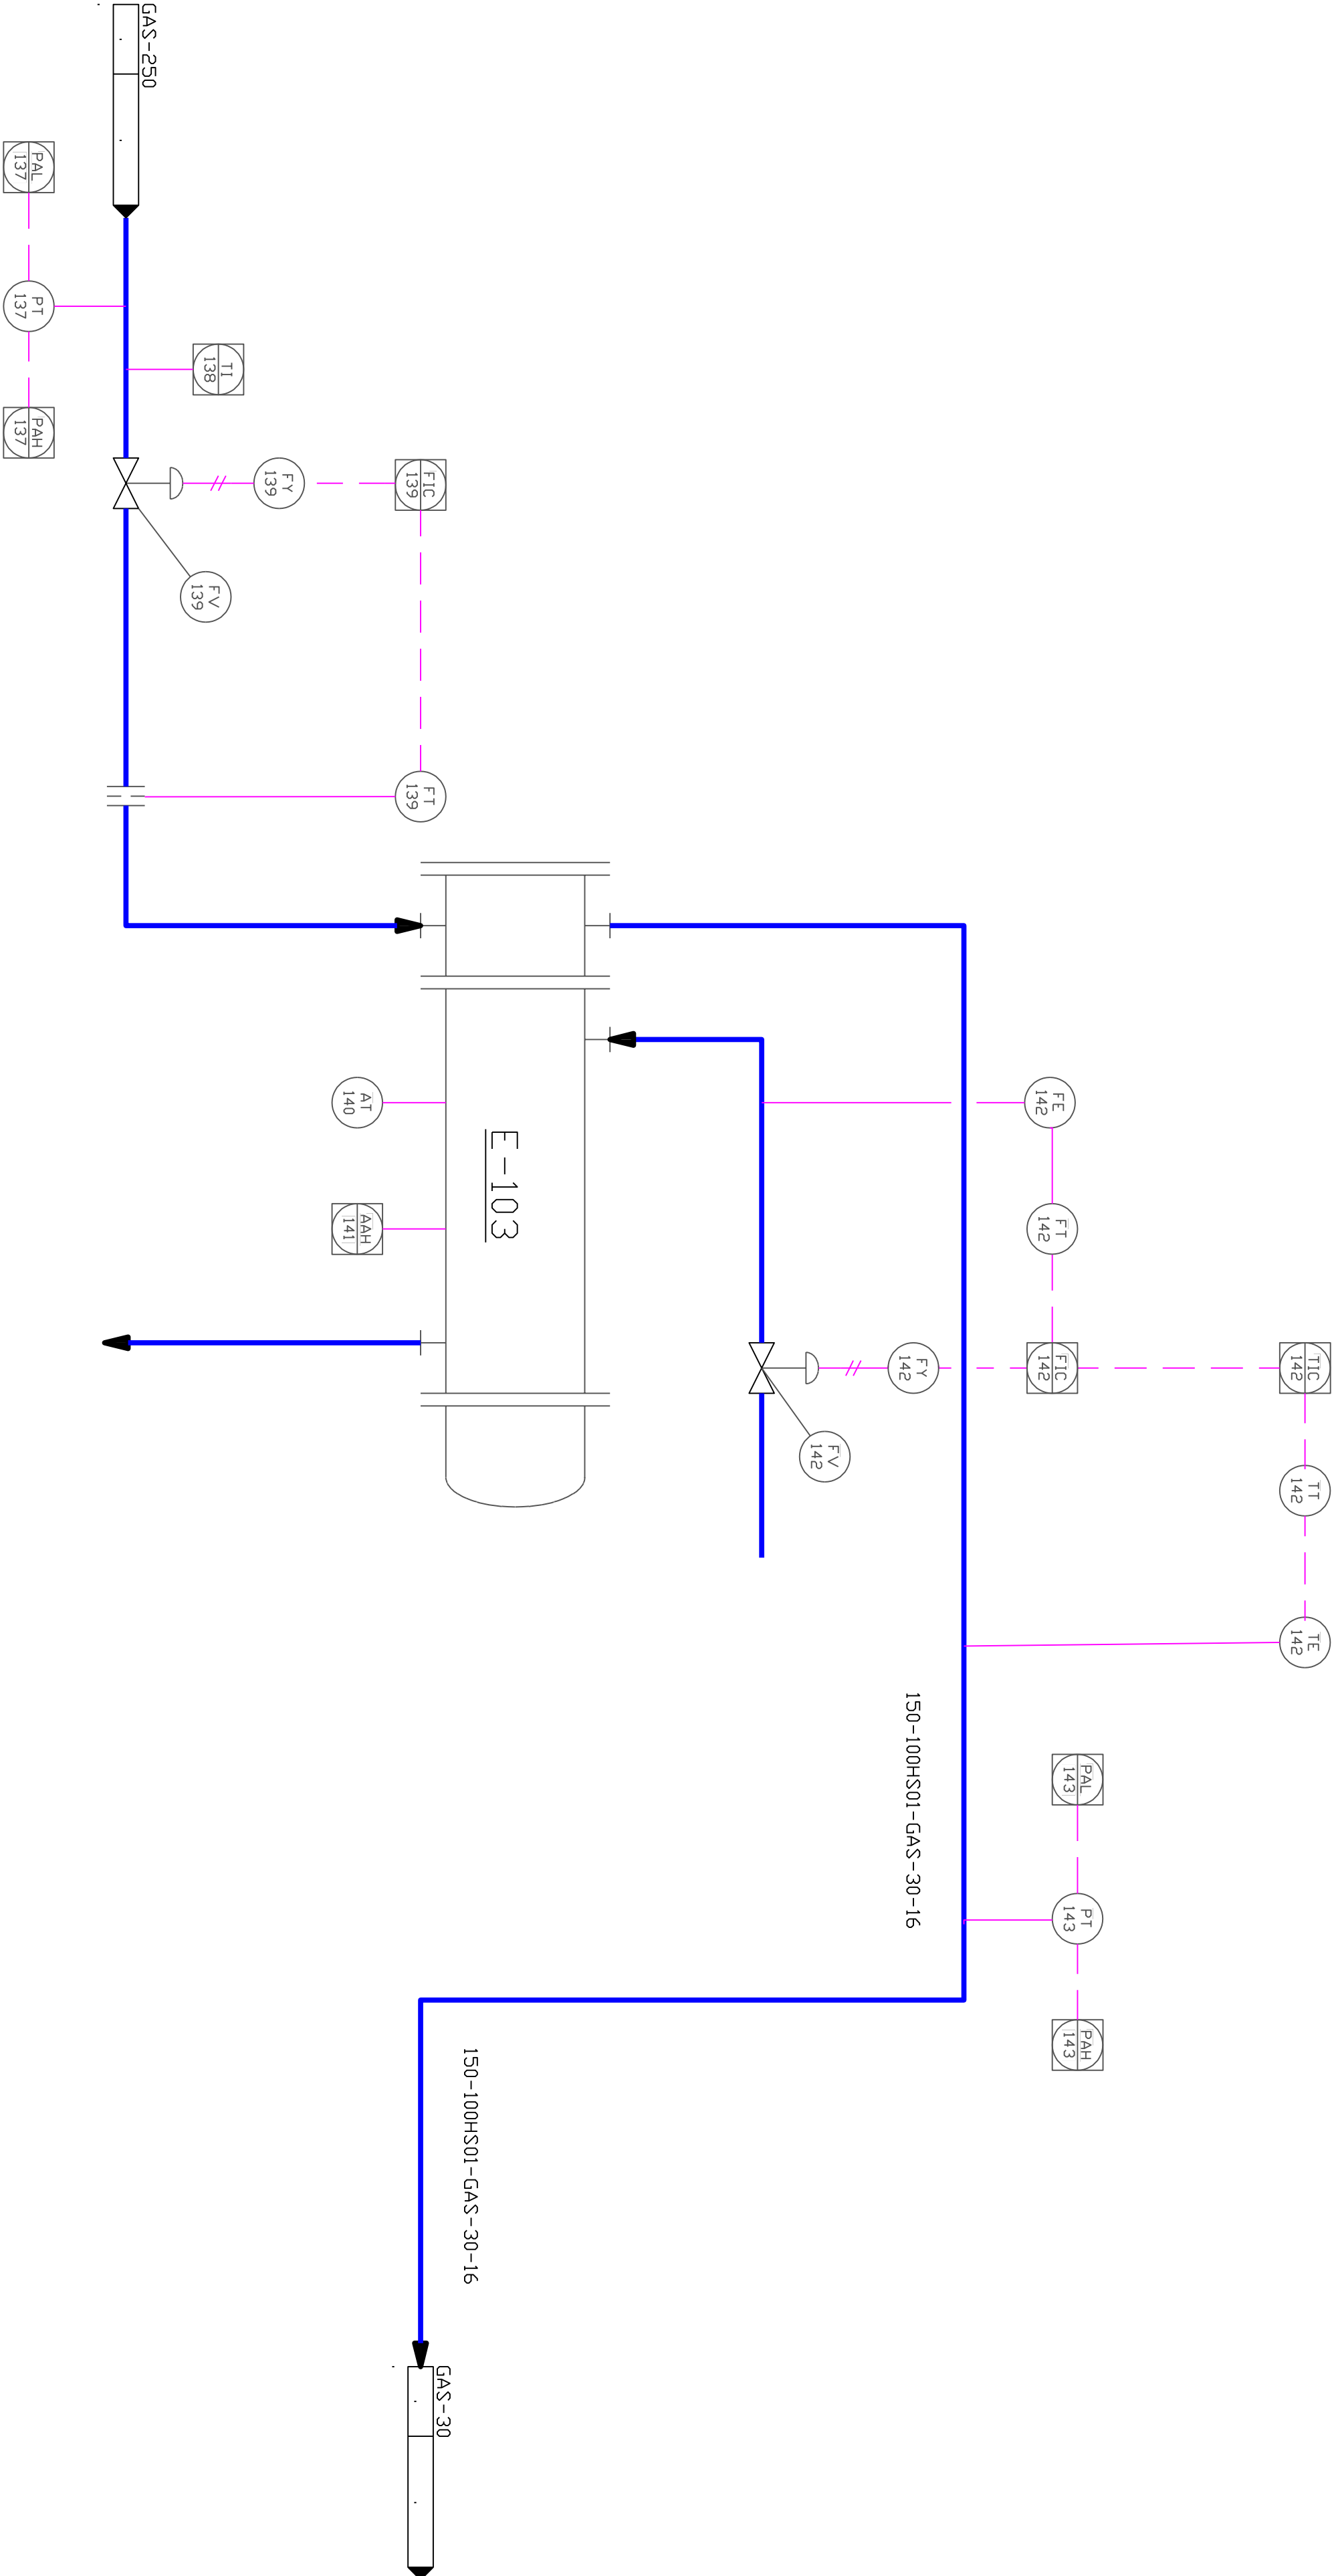

General Notes

- Intercambiador de calor
- Valvula de control
- AAH Alarma de analito alto
- AI Transmisor de analito
- TE Elemento de temperatura
- PAH Alarma de presión baja
- FIC Controlador indicador de flujo
- FV Convertidor de señal de flujo
- FE Elemento de flujo
- FI Transmisor de flujo
- PI Transmisor de presión
- PAH Alarma de presión alta
- FIC Controlador indicador de flujo
- FV Convertidor de señal de presión
- TIC Controlador indicador de temperatura
- TI Indicador de temperatura

No.	Revision/Issue	Date

Drawing Name
Segundo enfriador
del reactor

Project Name and Address

ANILINA
Planta de Anilina

Area	###	Stamp
Drawing Number	###	
Author	C6H6_	