



V-101: Separador líquido-vapor  
Parte superior: Hidrogeno  
Parte inferior: Mezcla orgánica y agua

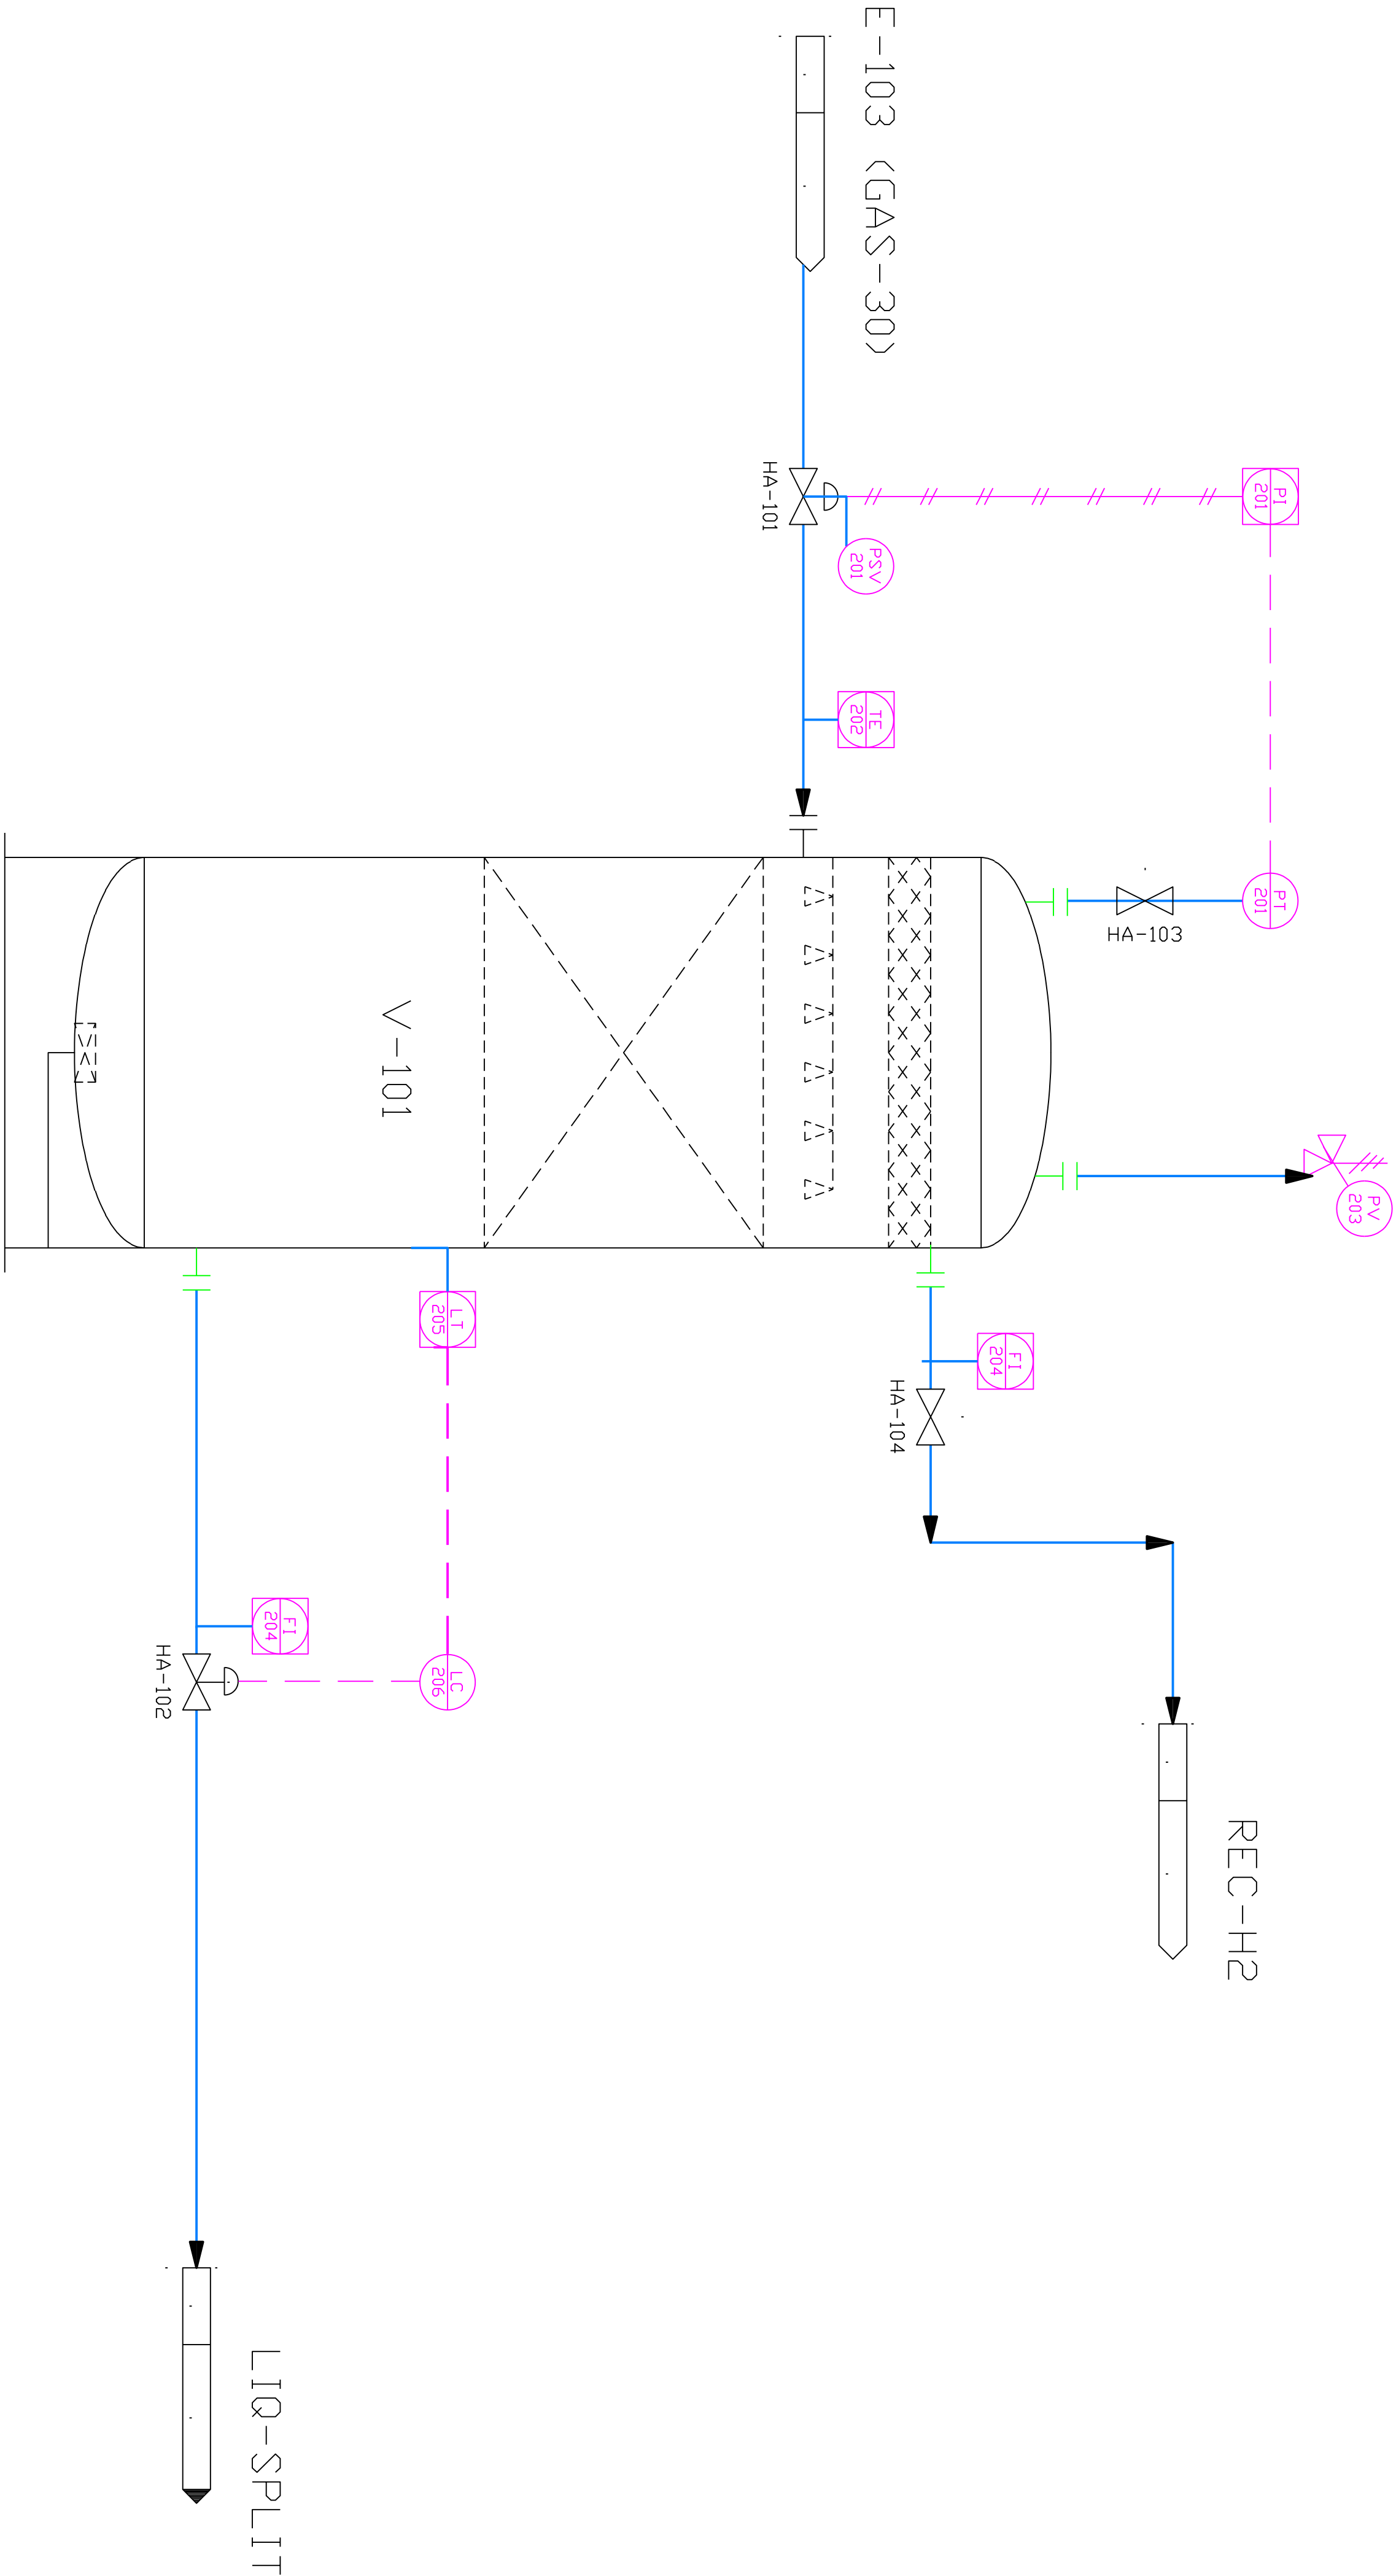


General Notes

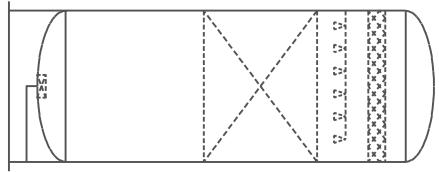

Separador

Valvula de compuerta

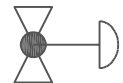

Valvula de control



Elemento de temperatura



Indicador de flujo



Indicador de presión



Transmisor de nivel



Controlador de nivel

|     |                |      |
|-----|----------------|------|
|     |                |      |
| No. | Revision/Issue | Date |

Drawing Name

Separador 001

####

Project Name and Address

ANILINA

Planta de Anilina

---

---

|                |            |       |
|----------------|------------|-------|
| Area           | ####       | Stamp |
| Drawing Number | ####       |       |
| Author         | IPN ESIOIE |       |