


TK-001: Tanque de mezcla de H2

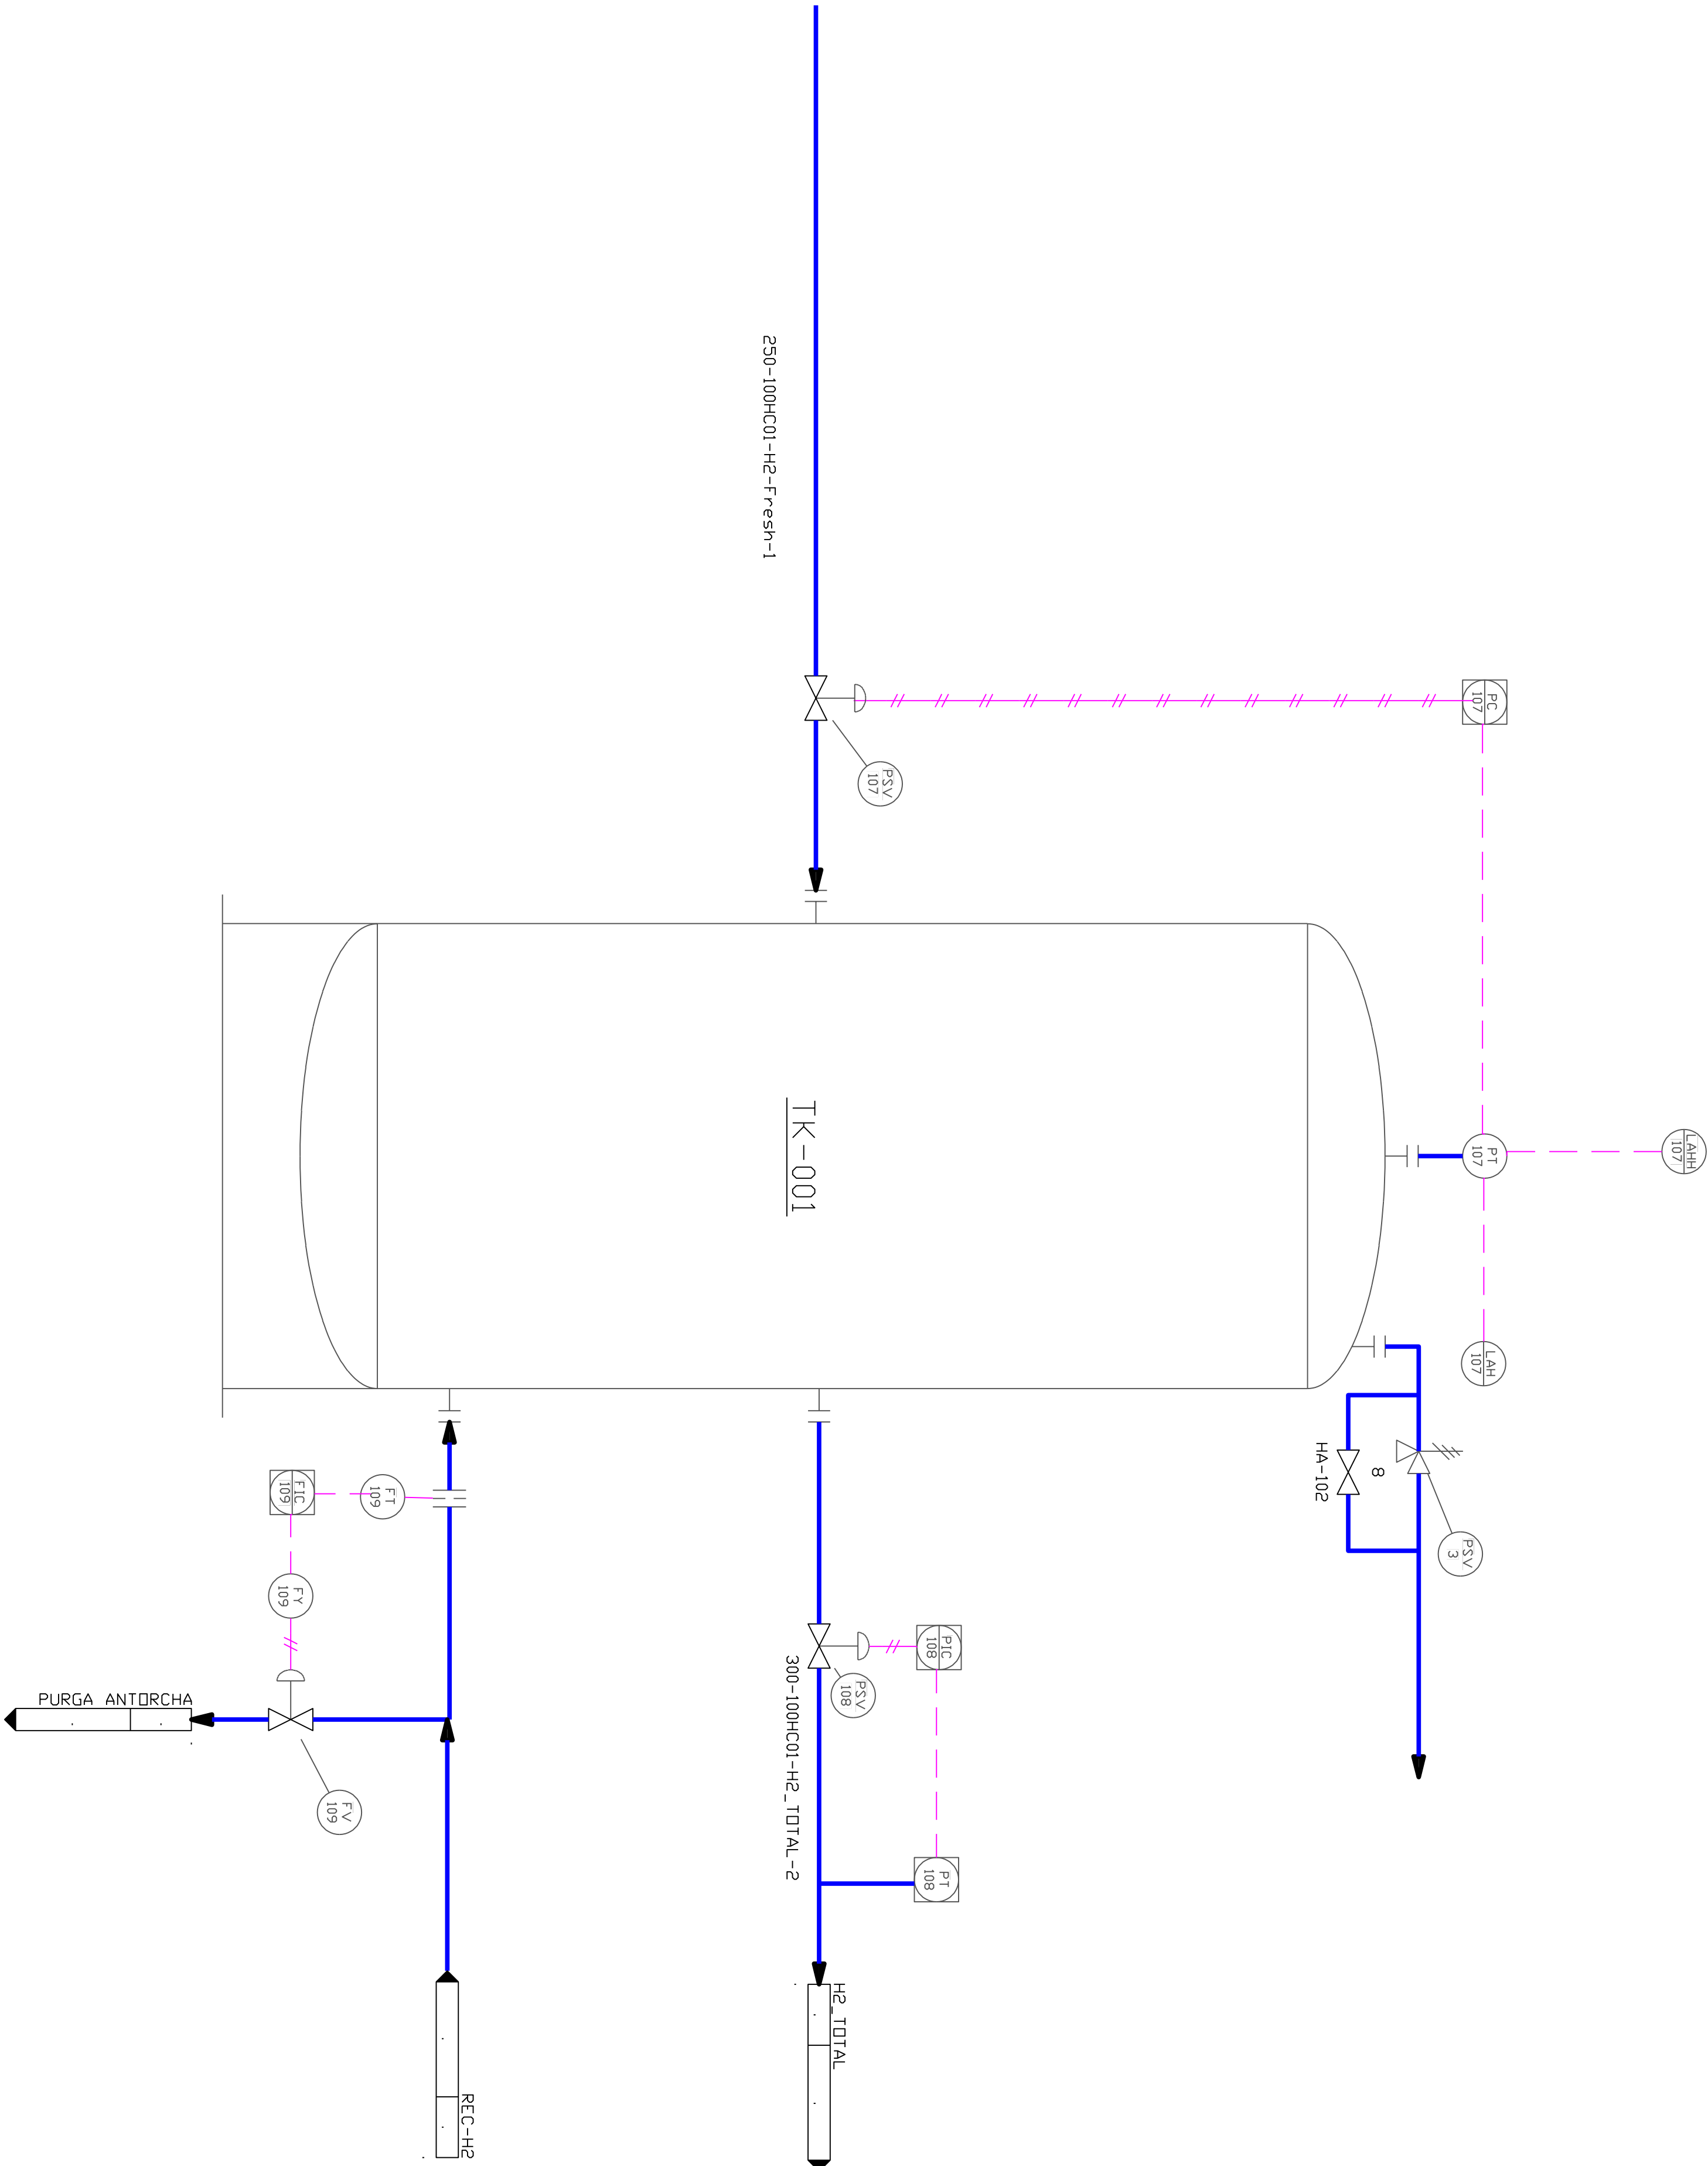

General Notes

TK-001
Tanque de
mezcla

Válvula de seguridad
por presión

Controlador de
presión

Controlador
indicador de presión

Transmisor de
presión

Alarma de nivel alto

Alarma de nivel alto

Válvula de control

Válvula de alivio

Válvula de compuerta

No.	Revision/Issue	Date

Drawing Name

Tanque hidrógeno

Project Name and Address

ANILINA
Planta de Anilina

Area

Tanque H2

Drawing Number

1

Author

ESIQIE IPN