


FLR-001
Antorcha

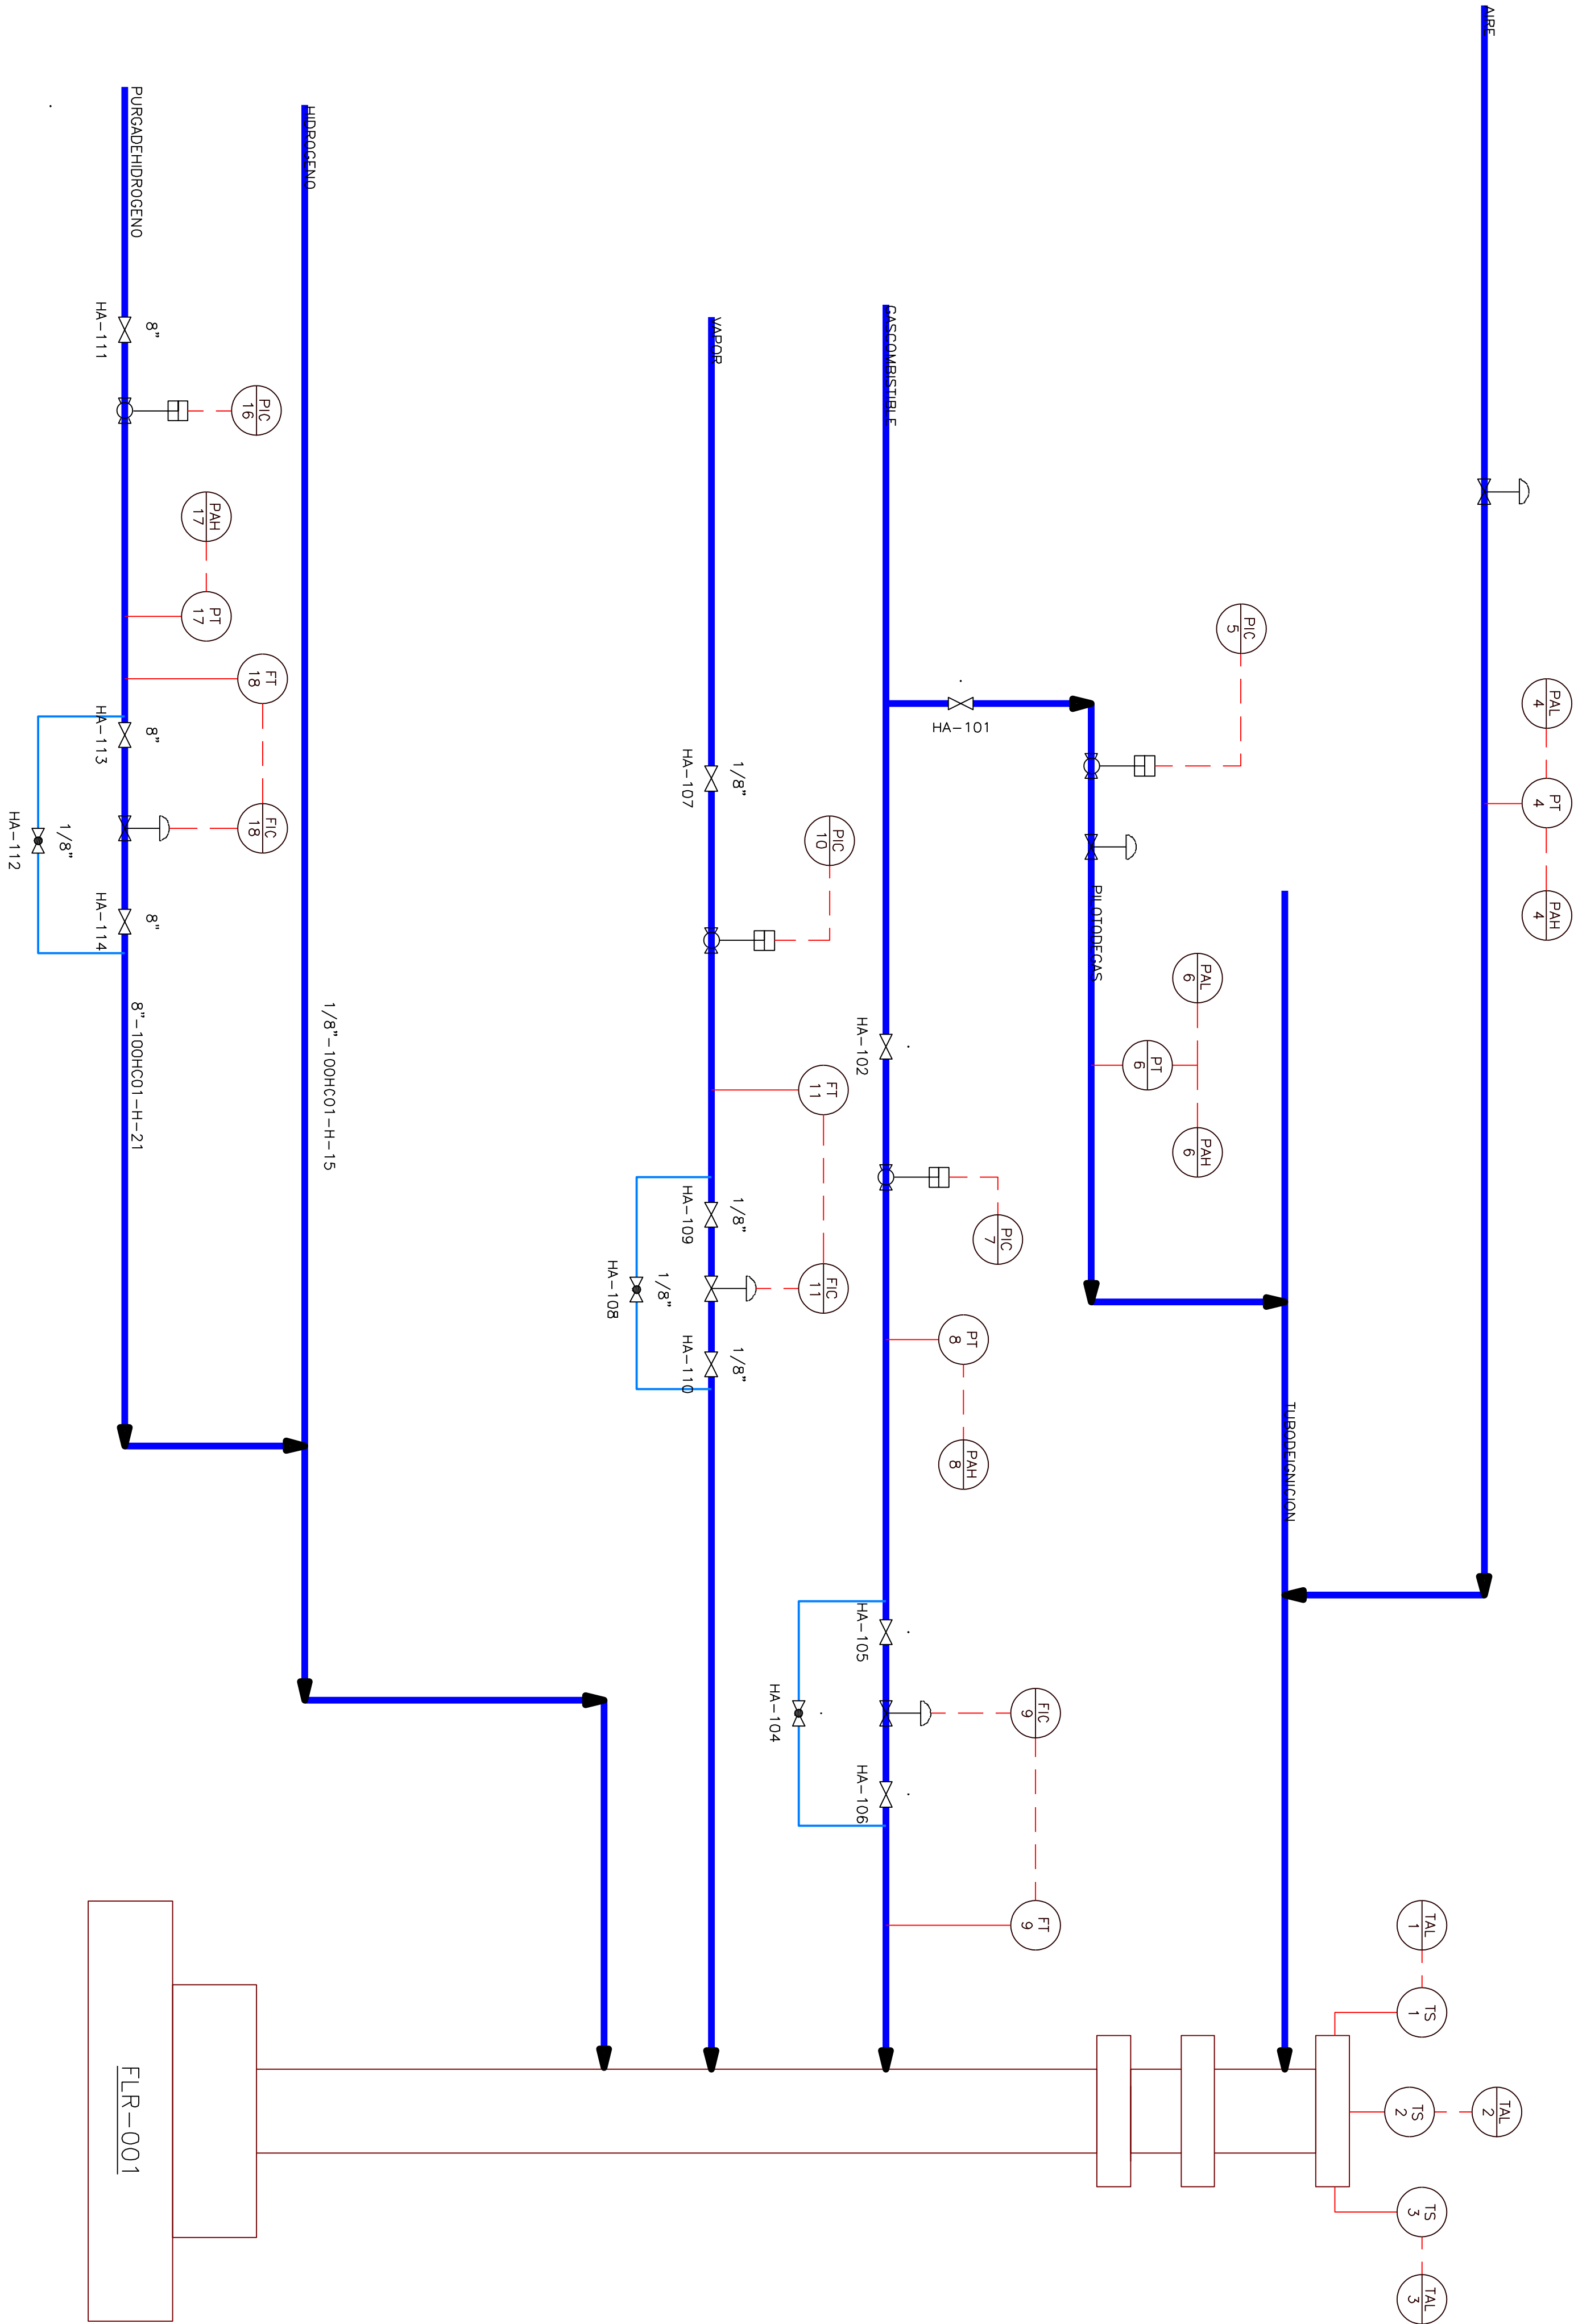

General Notes

- Antorcha
- Valvula de compuerta
- Valvula de control de flujo
- Valvula de control de presión
- Alarma de temperatura baja
- Controlador indicador de presión
- Alarma de presión alta
- Transmisor de presión
- Transmisor de flujo
- Instrumento de control de flujo
- Alarma de presión baja
- Switch de temperatura

No.	Revision/Issue	Date

ANTORCHA

Project Name and Address

ANILINA
Planta de Anilina

Area

###

Drawing Number

###

Author

ESQIE