


Columna de
destilación T-100

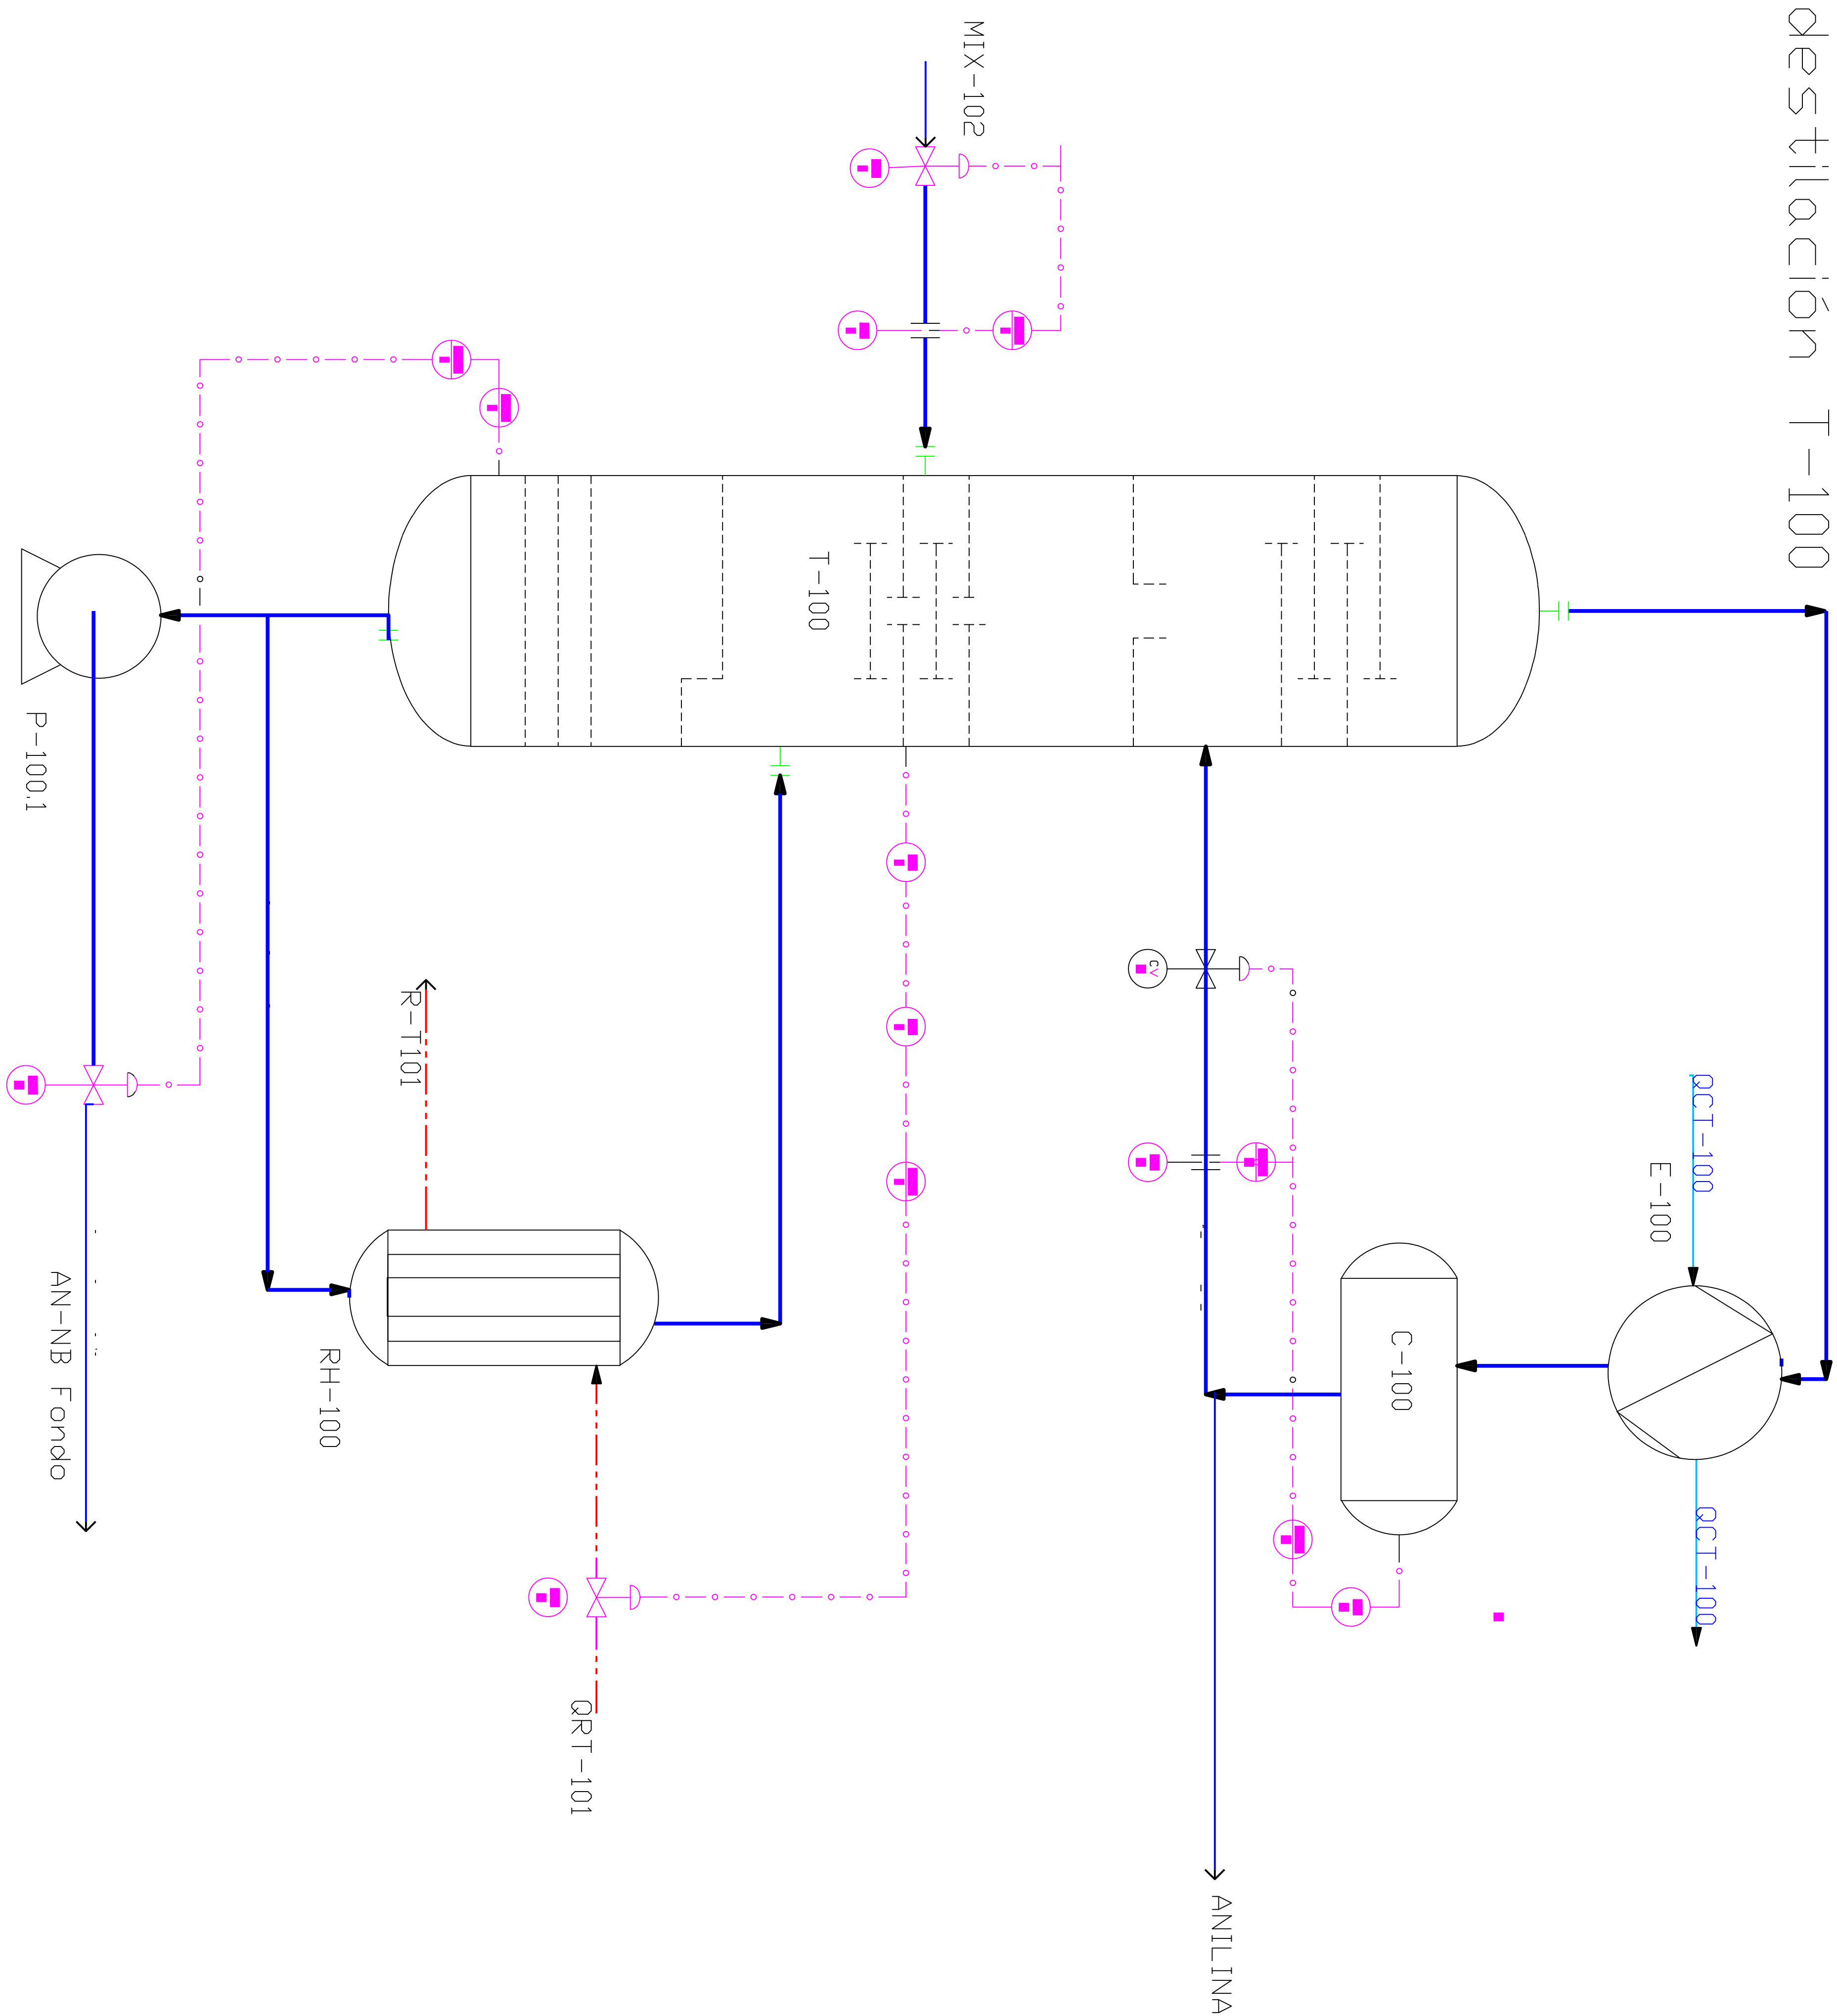

General Notes

- Rehervidor
- Columna de destilación
- Condensador parcial
- Tanque de destilado
- Valvula de control
- Transmisor de flujo
- Elemento de flujo
- Controlador de flujo
- Transmisor de presión
- Elemento de presión
- Controlador de presión
- Transmisor de temperatura
- Elemento de temperatura
- Controlador de temperatura

No.	Revision/Issue	Date

Drawing Name

COLUMNAT100

####

Project Name and Address

ANILINA

Planta de Anilina

Area	####	Stamp
Drawing Number	####	
Author	ESIQIE IPN	